


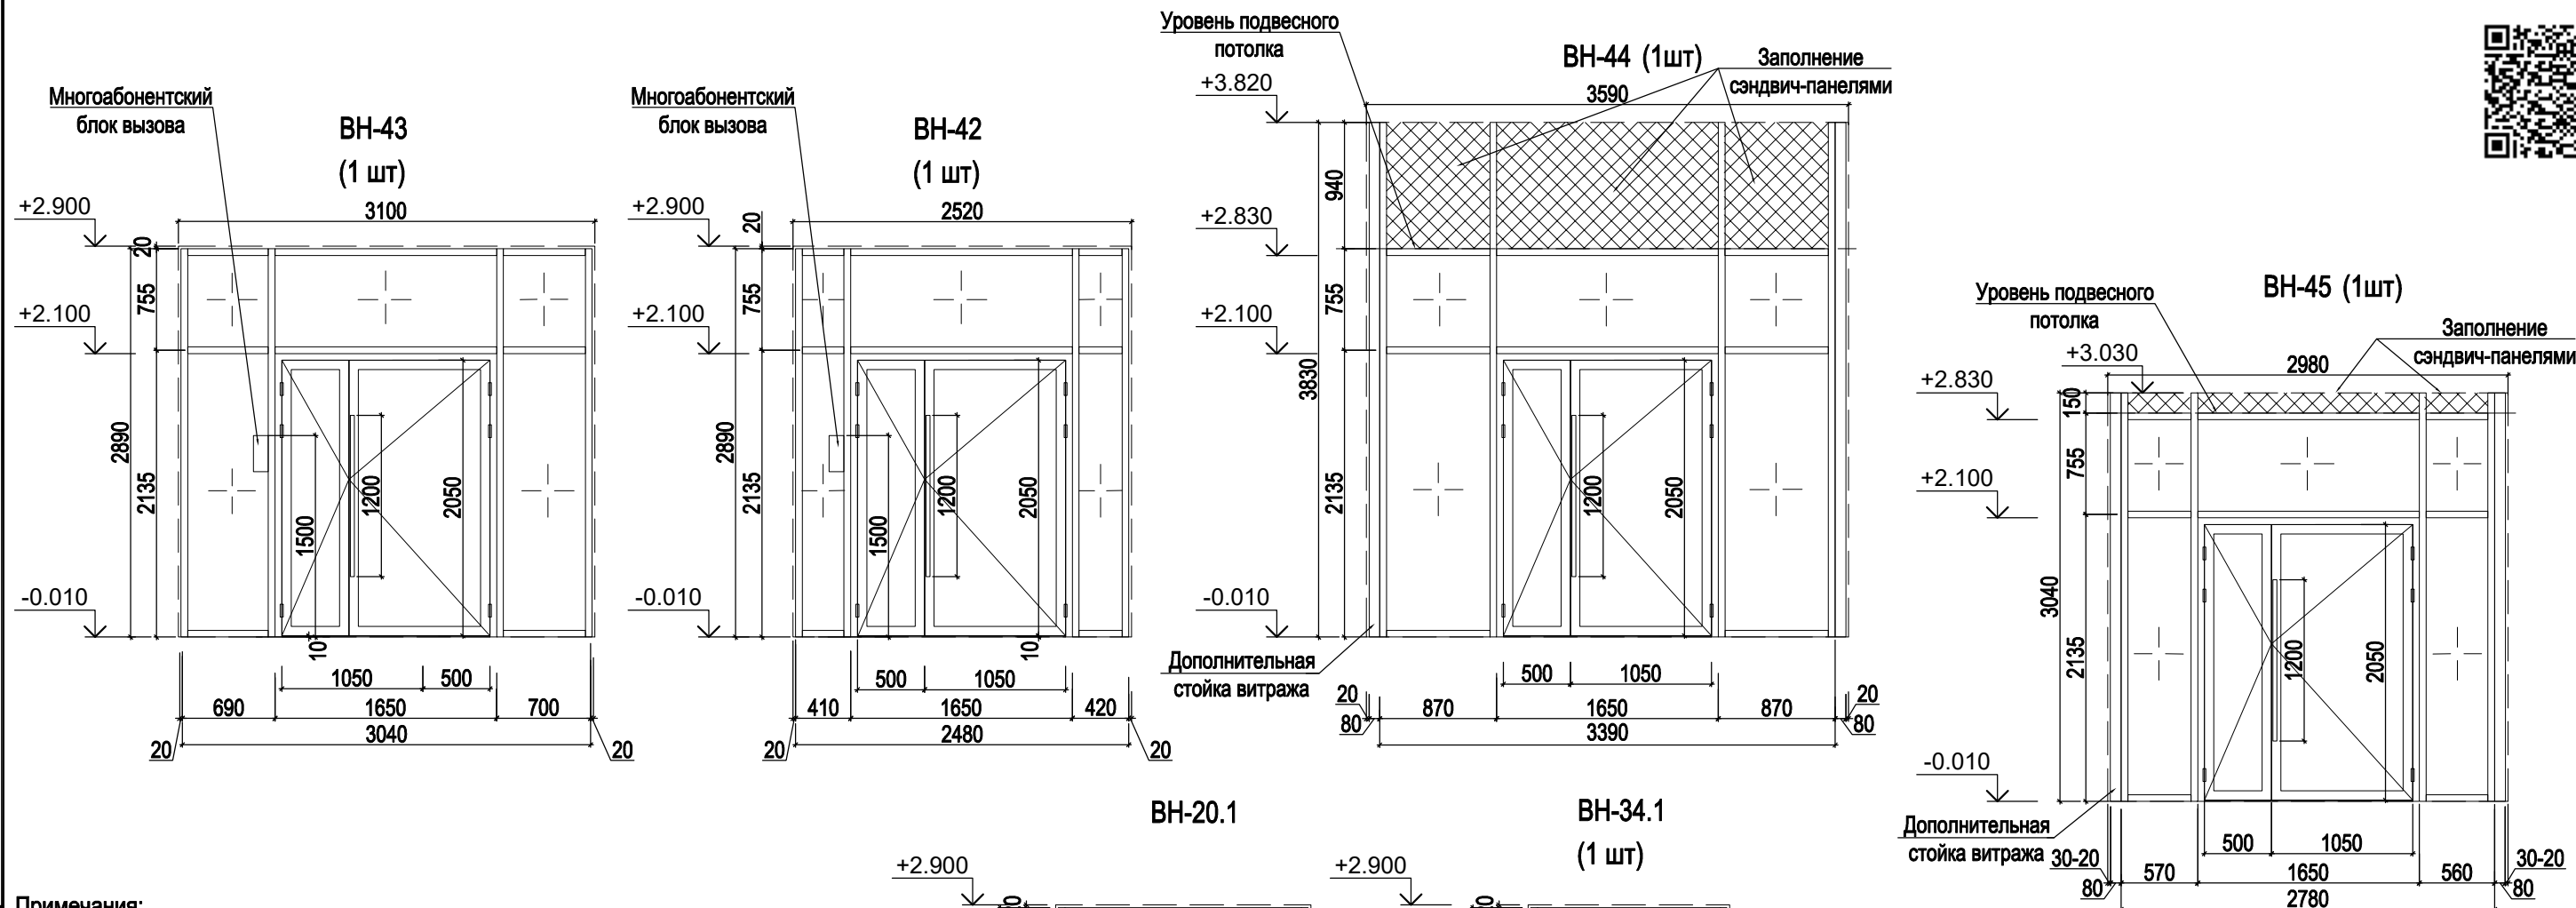

Примечания:

- Данный лист смотреть совместно с прочими листами данного раздела:
- планы 10/12/2022-АБ-4.2-АР1, АР2;
- фасады 10/12/2022-АБ-4.2-АР3;
- При выполнении витражных конструкций руководствоваться требованиями "Технических условий на применяемые материалы и инженерное оборудование" заказчика.
- Заполнение проемов осуществляется при участии производителя и осуществлении дополнительных замеров по месту.
- На схемах витражей указаны высотные отметки монтажные, вид на витражи дан с наружной стороны.
- Конструкция из алюминиевой профильной системы, остекленная. Приведенное сопротивление теплопередаче витражной конструкции не менее 0.6 м² С°/Вт.
Дверной блок: заполнение - однокамерный энергосберегающий стеклопакет с закаленными стеклами, армированное стекло по ходу эвакуации прозрачной пленкой класс защиты SM4, внутренний группы В, двупольный, правого(левого) открывания, с порогом не более 14мм, с доводчиком. Цвет профиля RAL 7016.
- Остекление витражей - Бесцветное прозрачное стекло с солнцезащитным напылением: Guardian SunGuard Silver 70/ AGC Stopsol Phoenix Clear или аналог.
- В зонах примыкания к проемам предусмотреть установку нащельников. Нащельники из оцинкованной стали толщиной не менее 0.5 мм. с полимерным покрытием по RAL7016.
- Перед установкой воздухозаборных решеток уточнить размеры проема по месту, смотреть совместно с разделом ОБ2.
- Вентиляционные решетки в системе витражной конструкции цвет: RAL 7016
- Предусмотреть ручки-скамьи высотой 1200 мм, цвет хром.
- Перед проектированием конструкций витражей изготовитель - разработчик (по согласованию с заказчиком) предоставляет расчет конструкций на восприятие горизонтальных и ветровых нагрузок. Шаг стоек и профилей уточняются изготовителем после контрольных замеров по месту. Заказ и монтаж изделий осуществляется после контрольных замеров и после согласования с Заказчиком и Генпроектировщиком
- Ширина проема в свету при открытой (основной) створке двери, должна составлять не менее 900мм, высота прохода в свету не менее 2000мм. При двух открытых створках ширина проема в свету должна составлять не менее 1200мм
- В проемах дверей, доступных для МГН, допускаются пороги высотой не более 0,014 м. (основание п. 6.2.4 СП 59.13330.2020)

Условные обозначения

- Стекло - бесцветное прозрачное с солнцезащитным напылением: Guardian SunGuard Silver 70/ AGC Stopsol Phoenix Clear
- Глухая створка - бесцветное прозрачное с солнцезащитным напылением: Guardian SunGuard Silver 70/ AGC Stopsol Phoenix Clear
- Заполнение сэндвич панелями

ПРОВЕРЕНО
ТЕХНИЧЕСКИЙ ОТДЕЛ
12.12.2025
без проверки объемов
Сотрудник ТО _____

ООО "СПЕЦИАЛИЗИРОВАННЫЙ
ЗАСТРОЙЩИК "СЭТЛ СТАНДАРТ"
В производство работ
12.12.2025
ДОКУМЕНТ ПОДПИСАН
ЭЛЕКТРОННОЙ ПОДПИСЬЮ
Сертификат E9EA95EC37FF8C83F8906EA12956C21905745F60
Владелец Раментьев Иван Николаевич
Действителен с 15.01.2025 по 15.01.2026

						10/12/2022-АБ-4.2-АР3						
						г. Санкт-Петербург, Большой Смоленский проспект, кад.№78:12:0007021:3355						
2	1	Изм.	709/25		12.25							
Изм.	Кол. уч.	Лист	№ док.	Подпись	Дата							
Выполнил		Сергеев А.			08.24	Многоквартирный жилой дом со встроенными помещениями, встроенно - пристроенной подземной автостоянкой, встроенно-пристроенной ДОО на 100 мест (корпус 4)		Стадия	Лист	Листов		
ГАП		Дудник			08.24			P	6			
Проверил		Гужева Ю.			08.24							
ГИП		Сергеев Д.			08.24							
						Секции 2.1-2.3. Схемы теплых витражей 1-го этажа ВН-20.1, ВН-34.1, ВН-42-45. М1:50		ООО "Архитектурное бюро "Сэтл Сити" № 0618.01-2015-7810302725-П-031				
Н.Контроль		Сугак П.			08.24							