


Витраж В8х6

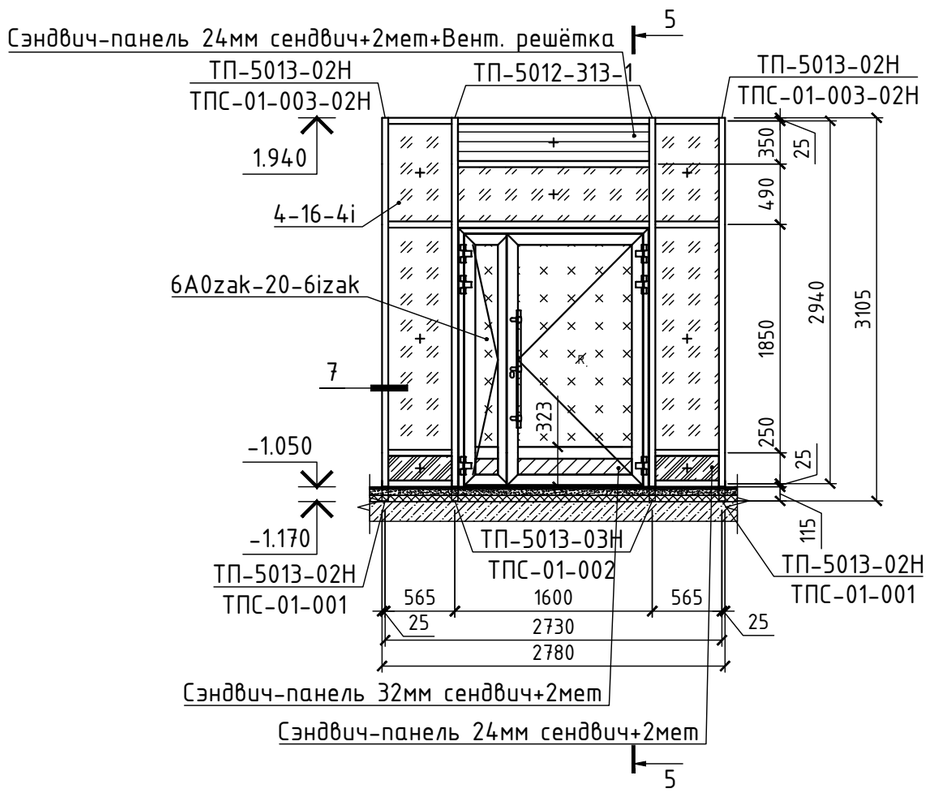

Витраж В8х7

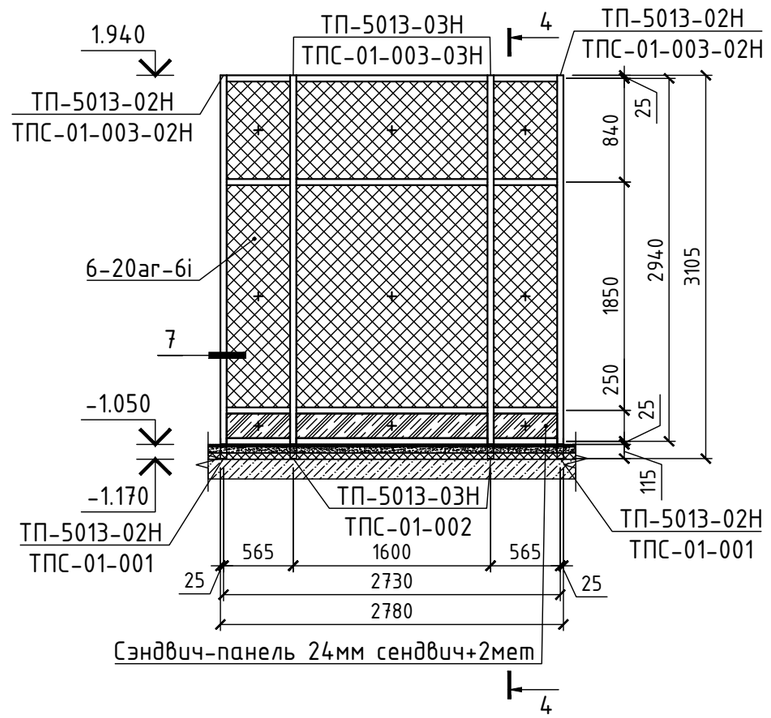

Витраж В8х8

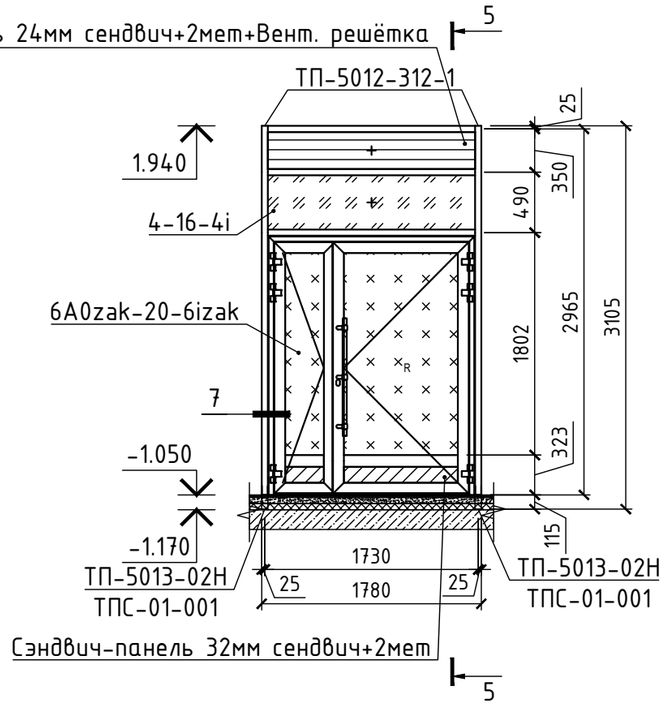

Ведомость заполнений

Наименование	УГО
Стеклопакет 4-16-4i	
Стеклопакет 6A0zak-20-6izak	
Стеклопакет 6-20ar-6i	
Сэндвич-панель 32мм сендвич+2мет	
Сэндвич-панель 24мм сендвич+2мет	
Сэндвич-панель 24мм сендвич+2мет+Вент. решётка	

Примечание

1. Общие данные смотри лист 2.
2. Спецификацию светопрозрачных конструкций смотри лист 25.
3. За отметку 0.000 на фасаде принят уровень чистого пола 1 этажа.
4. Каркасы витражей фасадная система ТП 50300, оконная серия с терморазрывом TWS 65, дверная серия с терморазрывом TDS 65.
5. Вид с фасада здания.
6. Покрытие профилей порошковая окраска RAL 7022.
7. Входные двери витражных конструкций удовлетворяют требованиям СП 59.13330.2016. Двери имеют ширину в свету при открывании одной створки не менее 0.9 м, при открывании двух створок в свету не менее 1.2 м. Нижняя часть дверных полотен на высоту не менее 0.3 м от уровня пола защищена противоударной полосой. Высота каждого элемента порога дверей не превышает 0.014 м.

Изм.	Кол.	Лист	№док.	Подпись	Дата	10-2024/Т77-3.1-КМ			
						Многоквартирные жилые дома со встроенными помещениями и подземными гаражами (автостоянками). 1, 2 этапы по адресу: г. Санкт-Петербург, посёлок Стрельна, проспект Будённого, участок 12 (кад. номер земельного участка 78:40:0019185:1188) 1 этап. Многоквартирные жилые дома со встроенными помещениями (корпус 3.1, 3.3, 3.4). Многоквартирный жилой дом с подземным гаражом (автостоянкой) (Корпус 3.1)			
Разработал		Степочкин			10.2024	Жилой дом. Корпус 3.1	Стадия	Лист	Листов
Проверил		Баркалов			10.2024		Р	19	
Н.контр.		Баркалов			10.2024	Витраж В8х6; В8х7; В8х8	ГК "Технология"		

Согласовано:

Взам. инв. №

Подпись и дата

Инв. № подл.

11.04.2025 г.

Формат А3