

Согласовано:

10.06.2026 г.	Инв. № подл.	Подпись и дата	Взам. инв. №

ООО "ГК Технология"

Стадия Р- Рабочая документация

"Многоквартирный жилой дом со встроенными помещениями" по адресу: Ленинградская область,
Всеволожский район, дер. Новосаратовка, кад. №47:07:0605001:1175 (участок 16 по ППТ)

Конструкции металлические

04-2026/Т-104-КМ

Генеральный директор ООО "ГК Технология"

_____ Храмов Н.В.

Технический директор ООО "ГК Технология"

_____ Баркалов Д.С.

2026 г


10.06.2026 г.
Согласовано:

Инв. № подл.
Подпись и дата
Взам. инв. №

ОБЩИЕ УКАЗАНИЯ

1. Крепление алюминиевых стоек витражей в проёмах производится на монтажные пластины с закладной клиновыми анкерами или универсальными анкерными болтами. Количество анкеров подобрано исходя из расчета.
2. Закладная F50.07.01 и монтажные пластины крепятся к основанию на два анкера.
3. Между монтажной пластиной и строительной частью прокладывается паронитовая прокладка толщиной 2 мм.
4. Вентиляция и отвод влаги с витража осуществляется в соответствии с техническими решениями указанными в альбоме завода изготовителя.
5. Заполнение световых проёмов: 4-20Ag-4i; 6-20Ag-6i; 6zak-18Ag-4i.4.2; 6zak-20Ag-6i; 6zak-20Ag-6zakRAL7024; Вент.реш.+сенд24+2мет; Сенд. 32мм+2мет.
6. Приведенное сопротивление теплопередаче конструкций не менее 0.6 м2°С/Вт.
7. Дверная фурнитура:
 - Ручка штанга хромированная 1200 из нержавеющей стали (или аналог);
 - Доводчик с задержкой закрывания до пяти секунд, RAL-7024;
 - Петля Ювенга Fast-3 (или аналог), RAL-7024;
 - Цилиндр Dogma CBR-1 35x55 ключ-ключ (или аналог);
 - Корпус замка Dogma 930a с валиком (или аналог);
 - Накладка Ювенга НД-26 (или аналог), RAL-7024;
 - Шпингалет Stublina 3060.00 (или аналог), RAL-7024;
 - Втулка шпингалет Stublina 3009.00 (или аналог);
 - Втулка шпингалет Stublina 3012.00 (или аналог);
 - Запорная планка Stublina 3016.00.220 (или аналог);
 - Фиксатор открывания двери типа «козья ножка», RAL-7024;
8. Антикоррозионная защита стальных изделий осуществляется согласно СП 28.13330.2017 (термодиффузионное покрытие t=45-60 мкм с перекрытием лакокрасочными покрытиями II и III групп).
9. Фасонные элементы выполнить из оцинкованной стали толщиной 0.5 мм RAL-7024.
10. Все используемые в конструкциях крепёжные детали (винты) изготовлены из нержавеющей стали или имеют антикоррозионную защиту.
11. В местах крепления козырьков к витражам предусмотрено усиление профиля закладным элементом.
12. Расчётная нагрузка на вырыв 1-го анкера клинового 8.66 кН. Все проведённые испытания отражены в протоколе испытаний. Протокол испытаний приложен в прилагаемых документах.

Схема крепления дверного блока

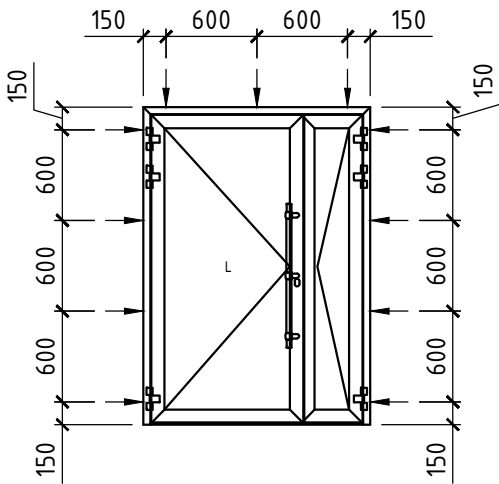

Условные обозначения

- > - анкерная пластина при монтаже в проём
- > - Нагрооп 4.8x70 HT-R бур при монтаже в витраж

						04-2026/Т-104-КМ			
						"Многоквартирный жилой дом со встроенными помещениями" по адресу: Ленинградская область, Всеволожский район, дер. Новосаратовка, кад. №47:07:0605001:1175 (участок 16 по ППТ)			
Изм.	Кол.	Лист	№ док.	Подпись	Дата				
Разработал		Степочкин			06.2026	Многоквартирный жилой дом со встроенными помещениями	Стадия	Лист	Листов
Проверил		Баркалов			06.2026		Р	3	
Н.контр.		Баркалов			06.2026	Общие указания	ГК "Технология"		

Ведомость чертежей основного комплекта		
Лист	Наименование	Примечание
1	Титульный лист	
2	Общие данные	
3	Общие указания	
4	Ведомость чертежей основного комплекта	
5	План 1 этажа. Секция 1	
6	План 1 этажа. Секция 2	
7	План 1 этажа. Секция 3	
8	План 1 этажа. Секция 4	
9	ВН-1.1.ВН-1.2.ВН1.3	
10	ВН-2.1.ВН-2.2.ВН2.3	
11	ВН-2.4.ВН-2.5.ВН2.6	
12	ВН-2.7.ВН-3.1.ВН-3.2	
13	ВН-3.3.ВН-3.4.ВН-3.5	
14	ВН-3.6.ВН-3.7.ВН-3.8	
15	ВН-3.9.ВН-4.1.ВН-4.2	
16	ВН-4.3.ВН-4.5.ВН-4.6	
17	ВН-4.7.ВН-4.8	
18	ВВ-1.1.ВВ-3.1.ВВ-3.2	
19	ВВ-4.1.ВВ-4.2	
20	Узлы 1-5	
21	Узлы 6-9	
22	Узлы 10-13	
23	Узлы 14-19	
24	Узел крепления закладной козырька	
25	Спецификация светопрозрачных конструкций	
26	Спецификация алюминиевого профиля	
27	Спецификация комплектующих (Начало)	
28	Спецификация комплектующих (Окончание)	
29	Спецификация уплотнителя	

						04-2026/Т-104-КМ				
						"Многоквартирный жилой дом со встроенными помещениями" по адресу: Ленинградская область, Всеволожский район, дер. Новосаратовка, кад. №47:07:0605001:1175 (участок 16 по ППТ)				
Изм.	Кол.	Лист	№ док.	Подпись	Дата					
						Многоквартирный жилой дом со встроенными помещениями		Стадия	Лист	Листов
Разработал		Степочкин			06.2026			Р	4	
Проверил		Баркалов			06.2026	Ведомость чертежей основного комплекта		ГК "Технология"		
Н.контр.		Баркалов			06.2026					

План 1 этажа
Секция 1

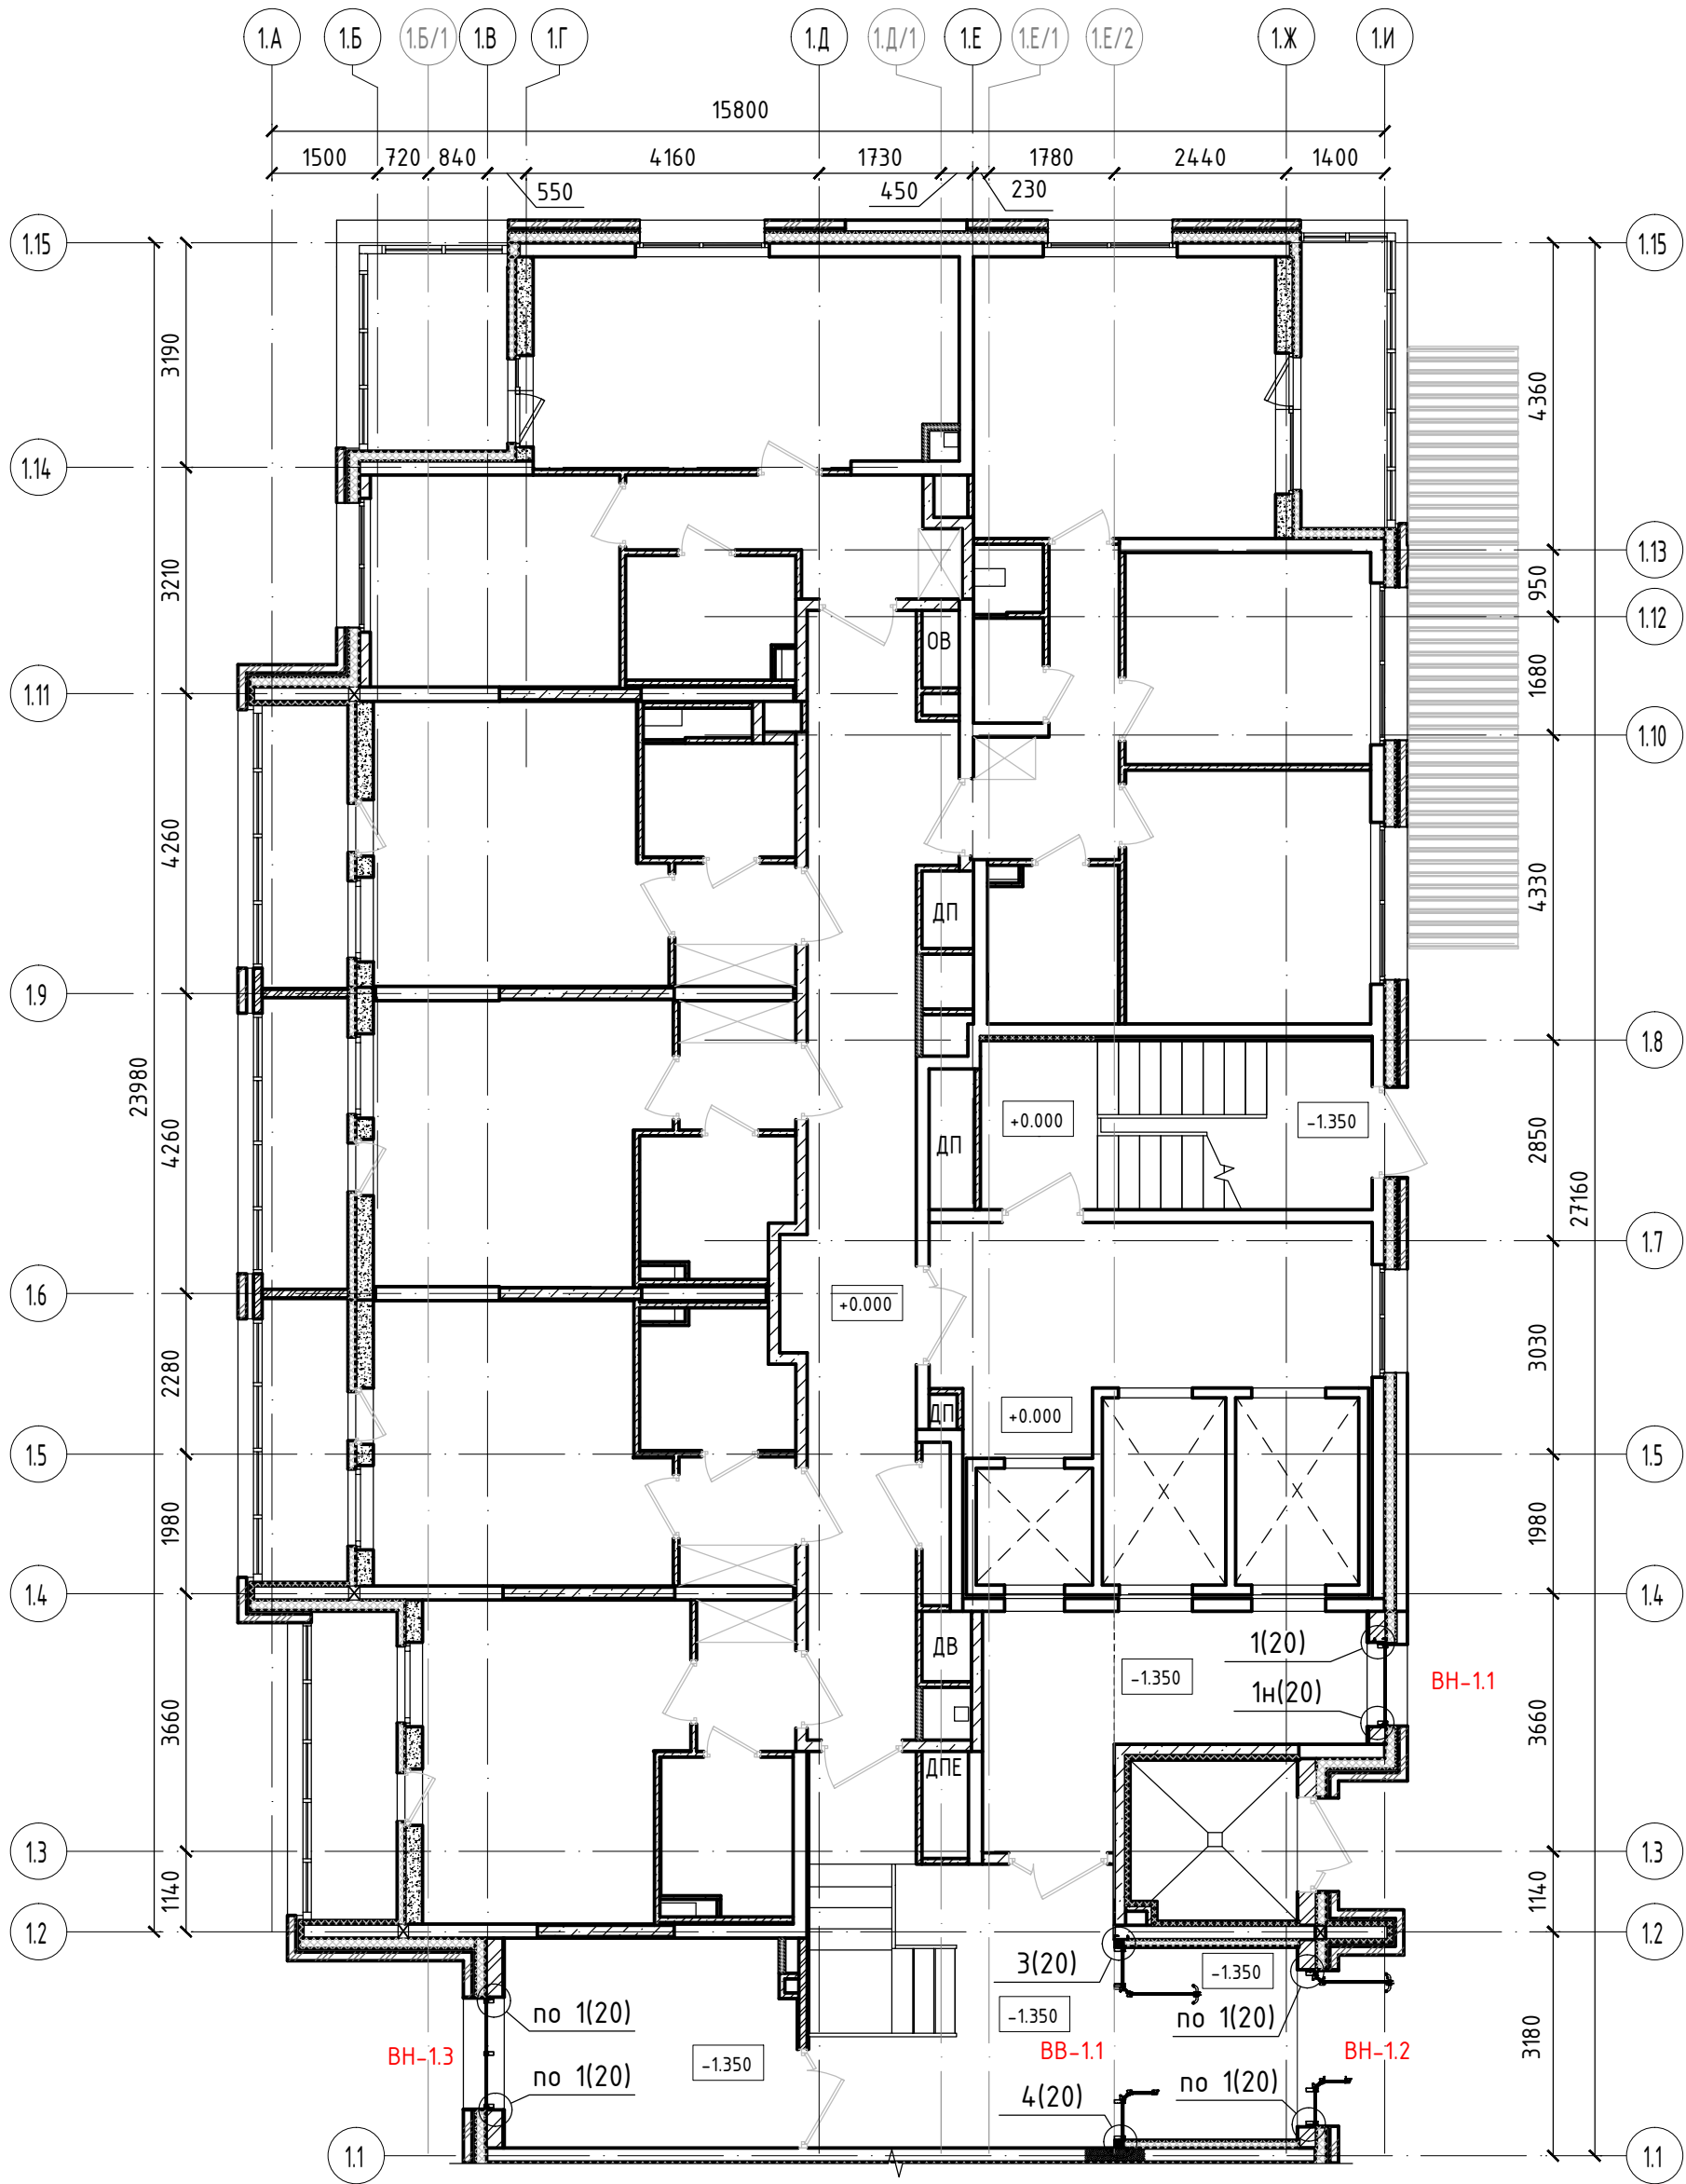


Схема расположения секций

Примечание

- Общие данные смотри лист 2.
- Спецификацию светопрозрачных конструкций смотри лист 25.

Изм.	Кол.	Лист	№ док.	Подпись	Дата
Разработал	Степочкин				06.2026
Проверил	Баркалов				06.2026
Н.контр.	Баркалов				06.2026

04-2026/Т-104-КМ		
"Многоквартирный жилой дом со встроенными помещениями" по адресу: Ленинградская область, Всеволожский район, дер. Новосаратовка, кад. №47:07:0605001:1175 (участок 16 по ППТ)		
Многоквартирный жилой дом со встроенными помещениями	Стадия	Лист
	Р	5
План 1 этажа. Секция 1	ГК "Технология"	

План 1 этажа
Секция 2


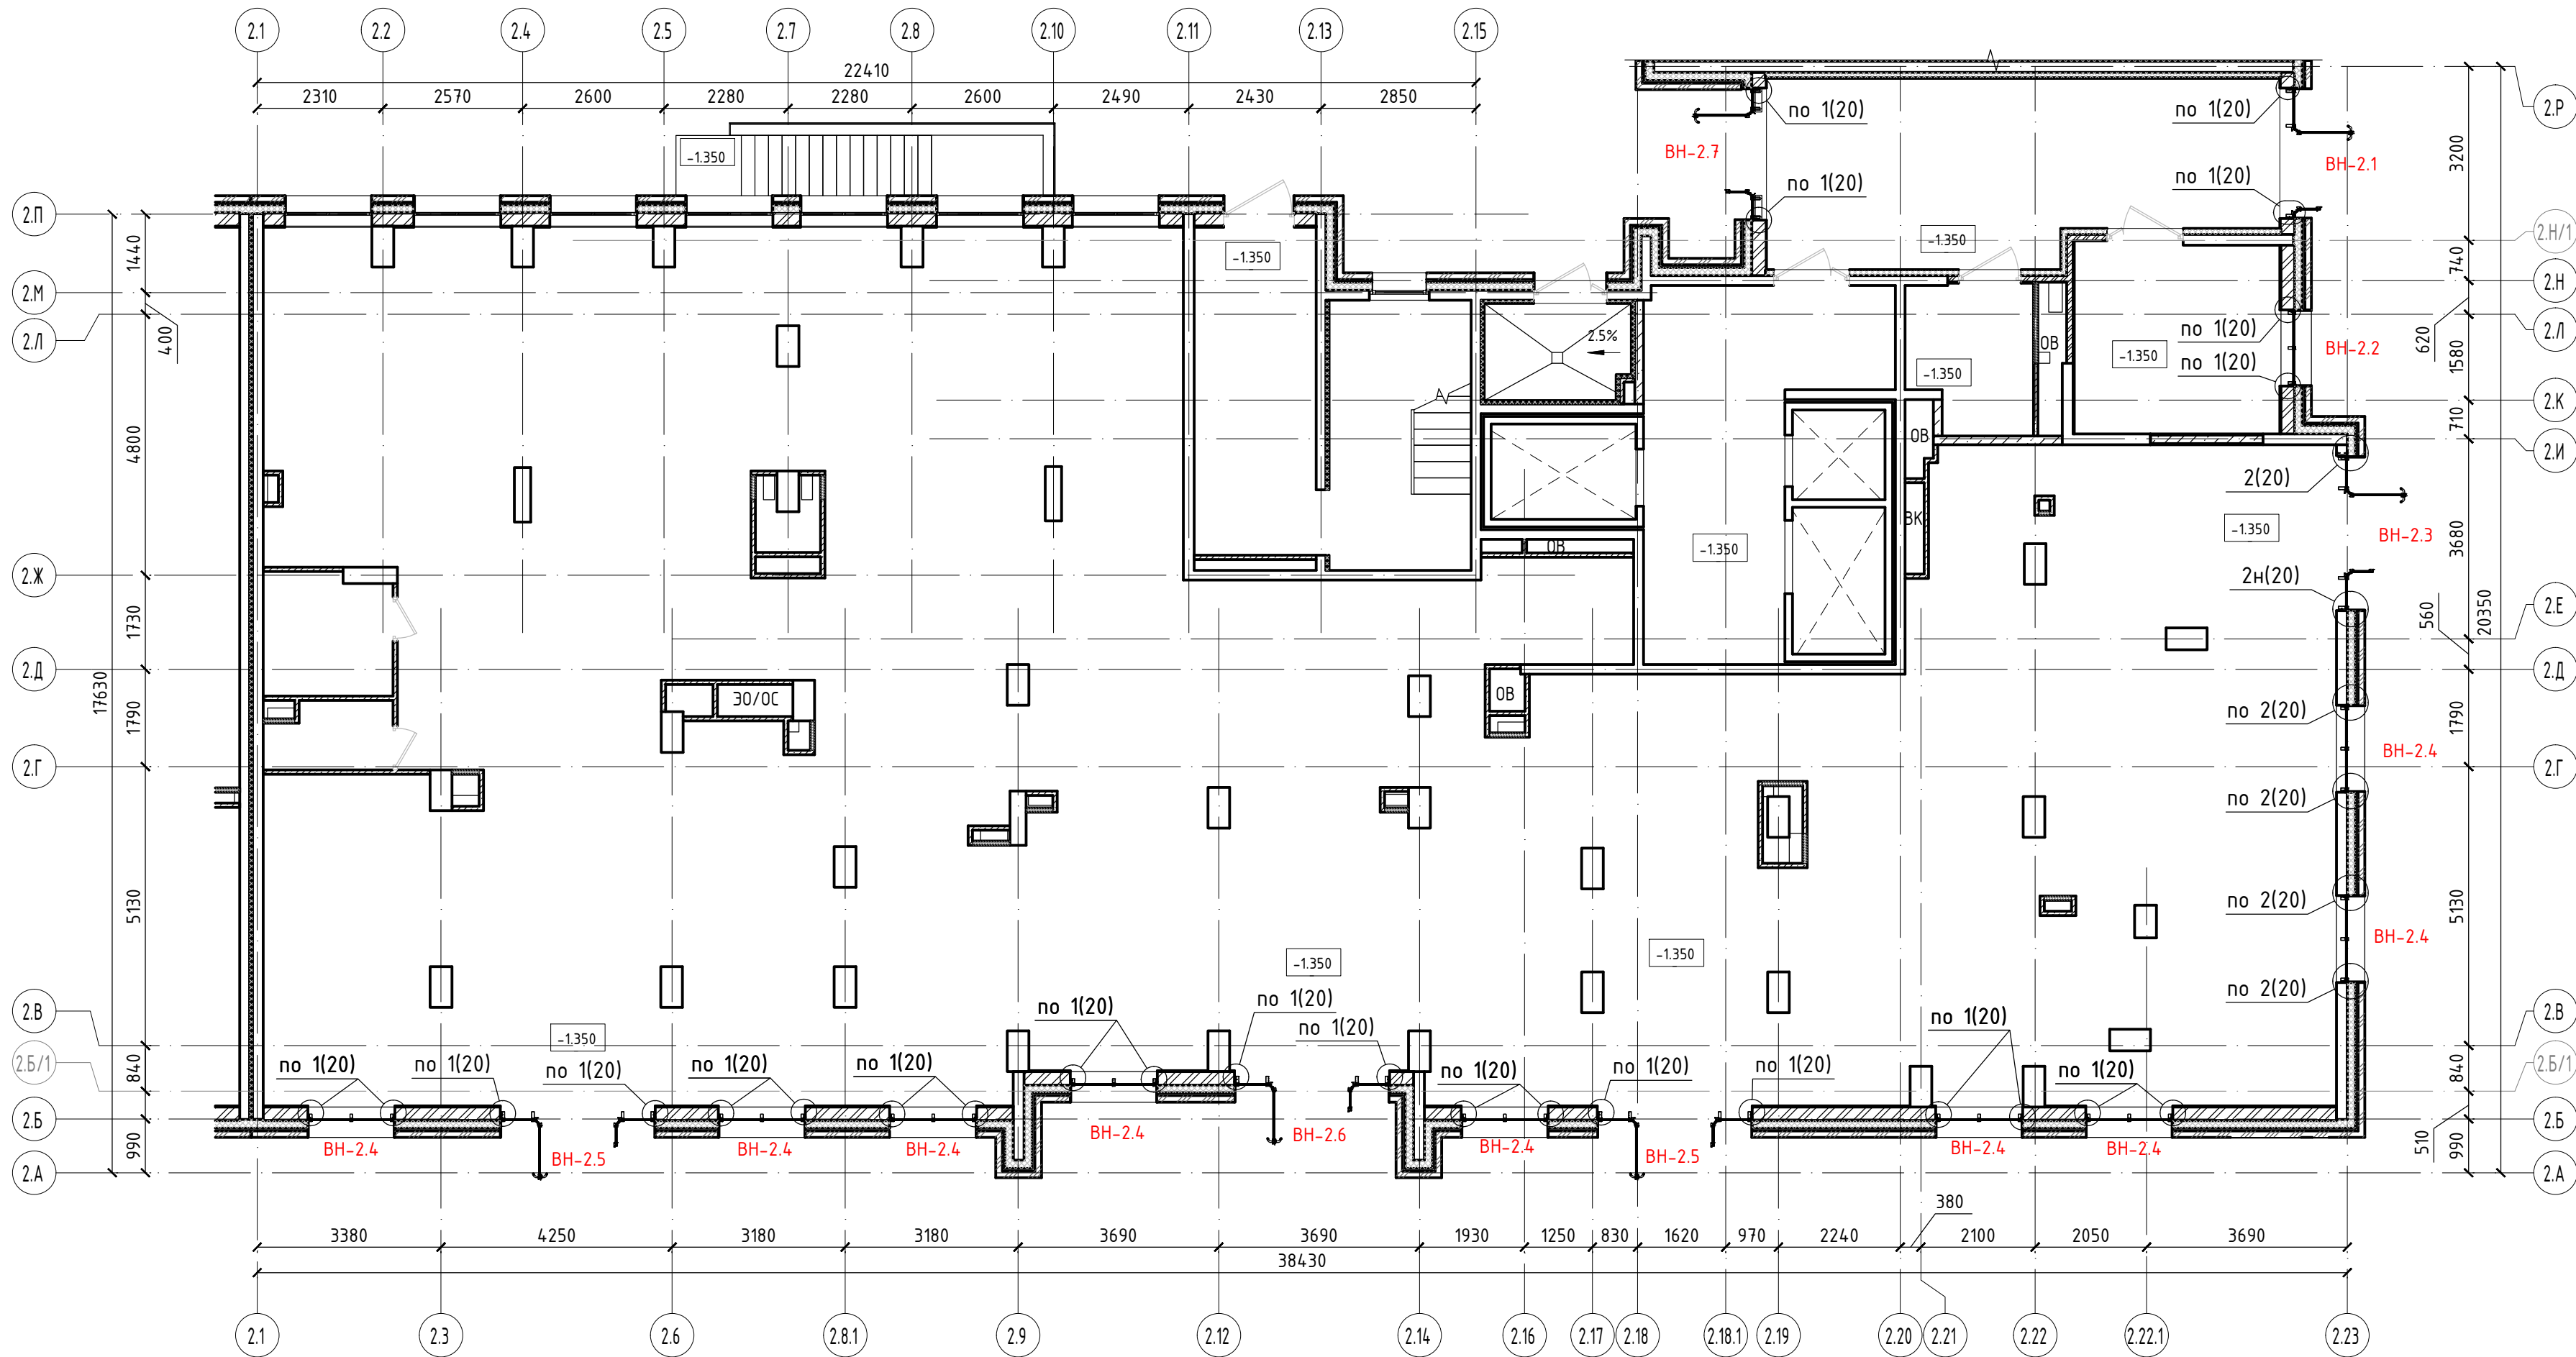


Схема расположения секций

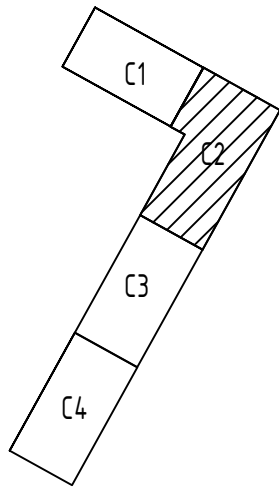

Примечание

- Общие данные смотри лист 2.
- Спецификацию светопрозрачных конструкций смотри лист 25.

						04-2026/Т-104-КМ			
						"Многоквартирный жилой дом со встроенными помещениями" по адресу: Ленинградская область, Всеволожский район, дер. Новосаратовка, кад. №47:07:0605001:1175 (участок 16 по ППТ)			
Изм.	Кол.	Лист	№ док.	Подпись	Дата	Многоквартирный жилой дом со встроенными помещениями	Стадия	Лист	Листов
Разработал	Степачкин				06.2026		Р	6	
Проверил	Баркалов				06.2026				
Н.контр.	Баркалов				06.2026	План 1 этажа. Секция 2		ГК "Технология"	

План 1 этажа
Секция 3


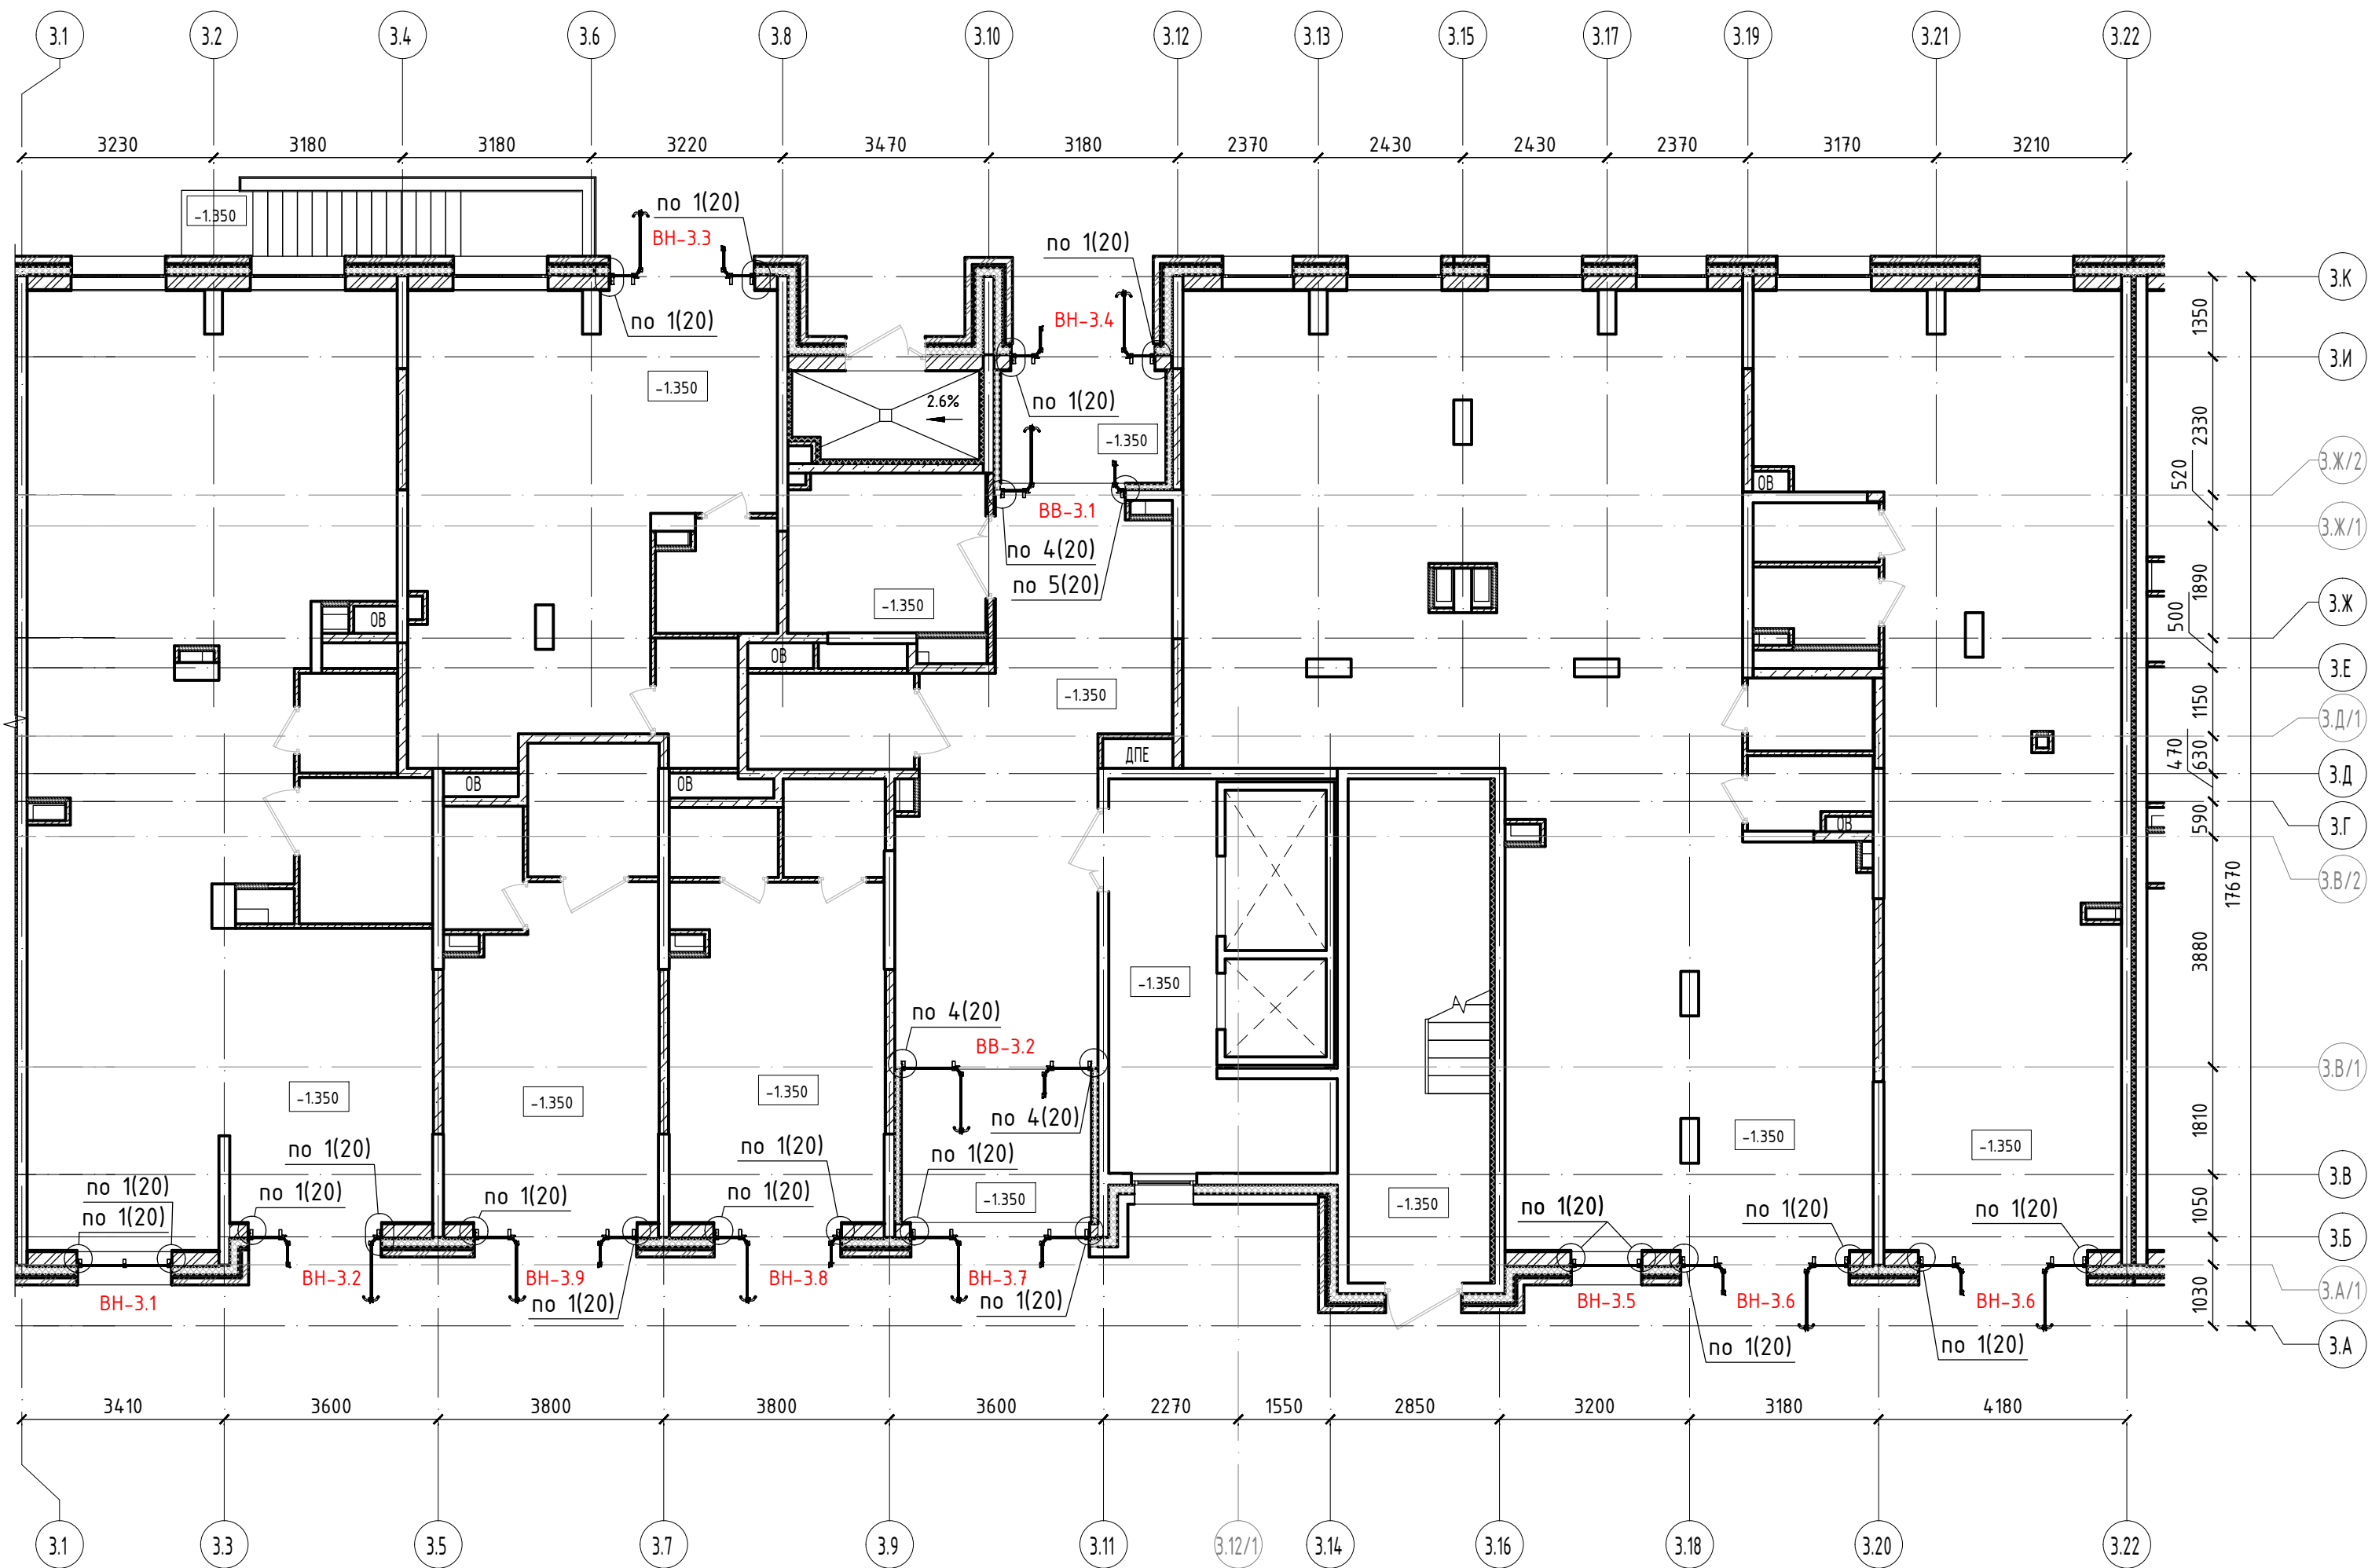


Схема расположения секций

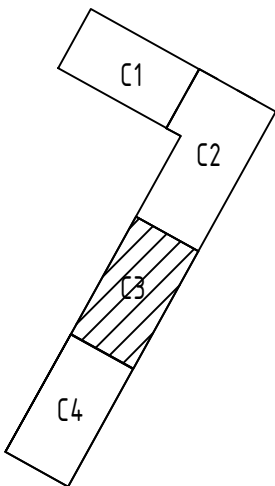

Примечание

- Общие данные смотри лист 2.
- Спецификацию светопрозрачных конструкций смотри лист 25.

						04-2026/Т-104-КМ			
						"Многоквартирный жилой дом со встроенными помещениями" по адресу: Ленинградская область, Всеволожский район, дер. Новосаратовка, кад. №47:07:0605001:1175 (участок 16 по ППТ)			
Изм.	Кол.	Лист	№ док.	Подпись	Дата	Многоквартирный жилой дом со встроенными помещениями	Стация	Лист	Листов
Разработал	Степачкин				06.2026		Р	7	
Проверил	Баркалов				06.2026	План 1 этажа. Секция 3		ГК "Технология"	
Н.контр.	Баркалов				06.2026				

Секция 4


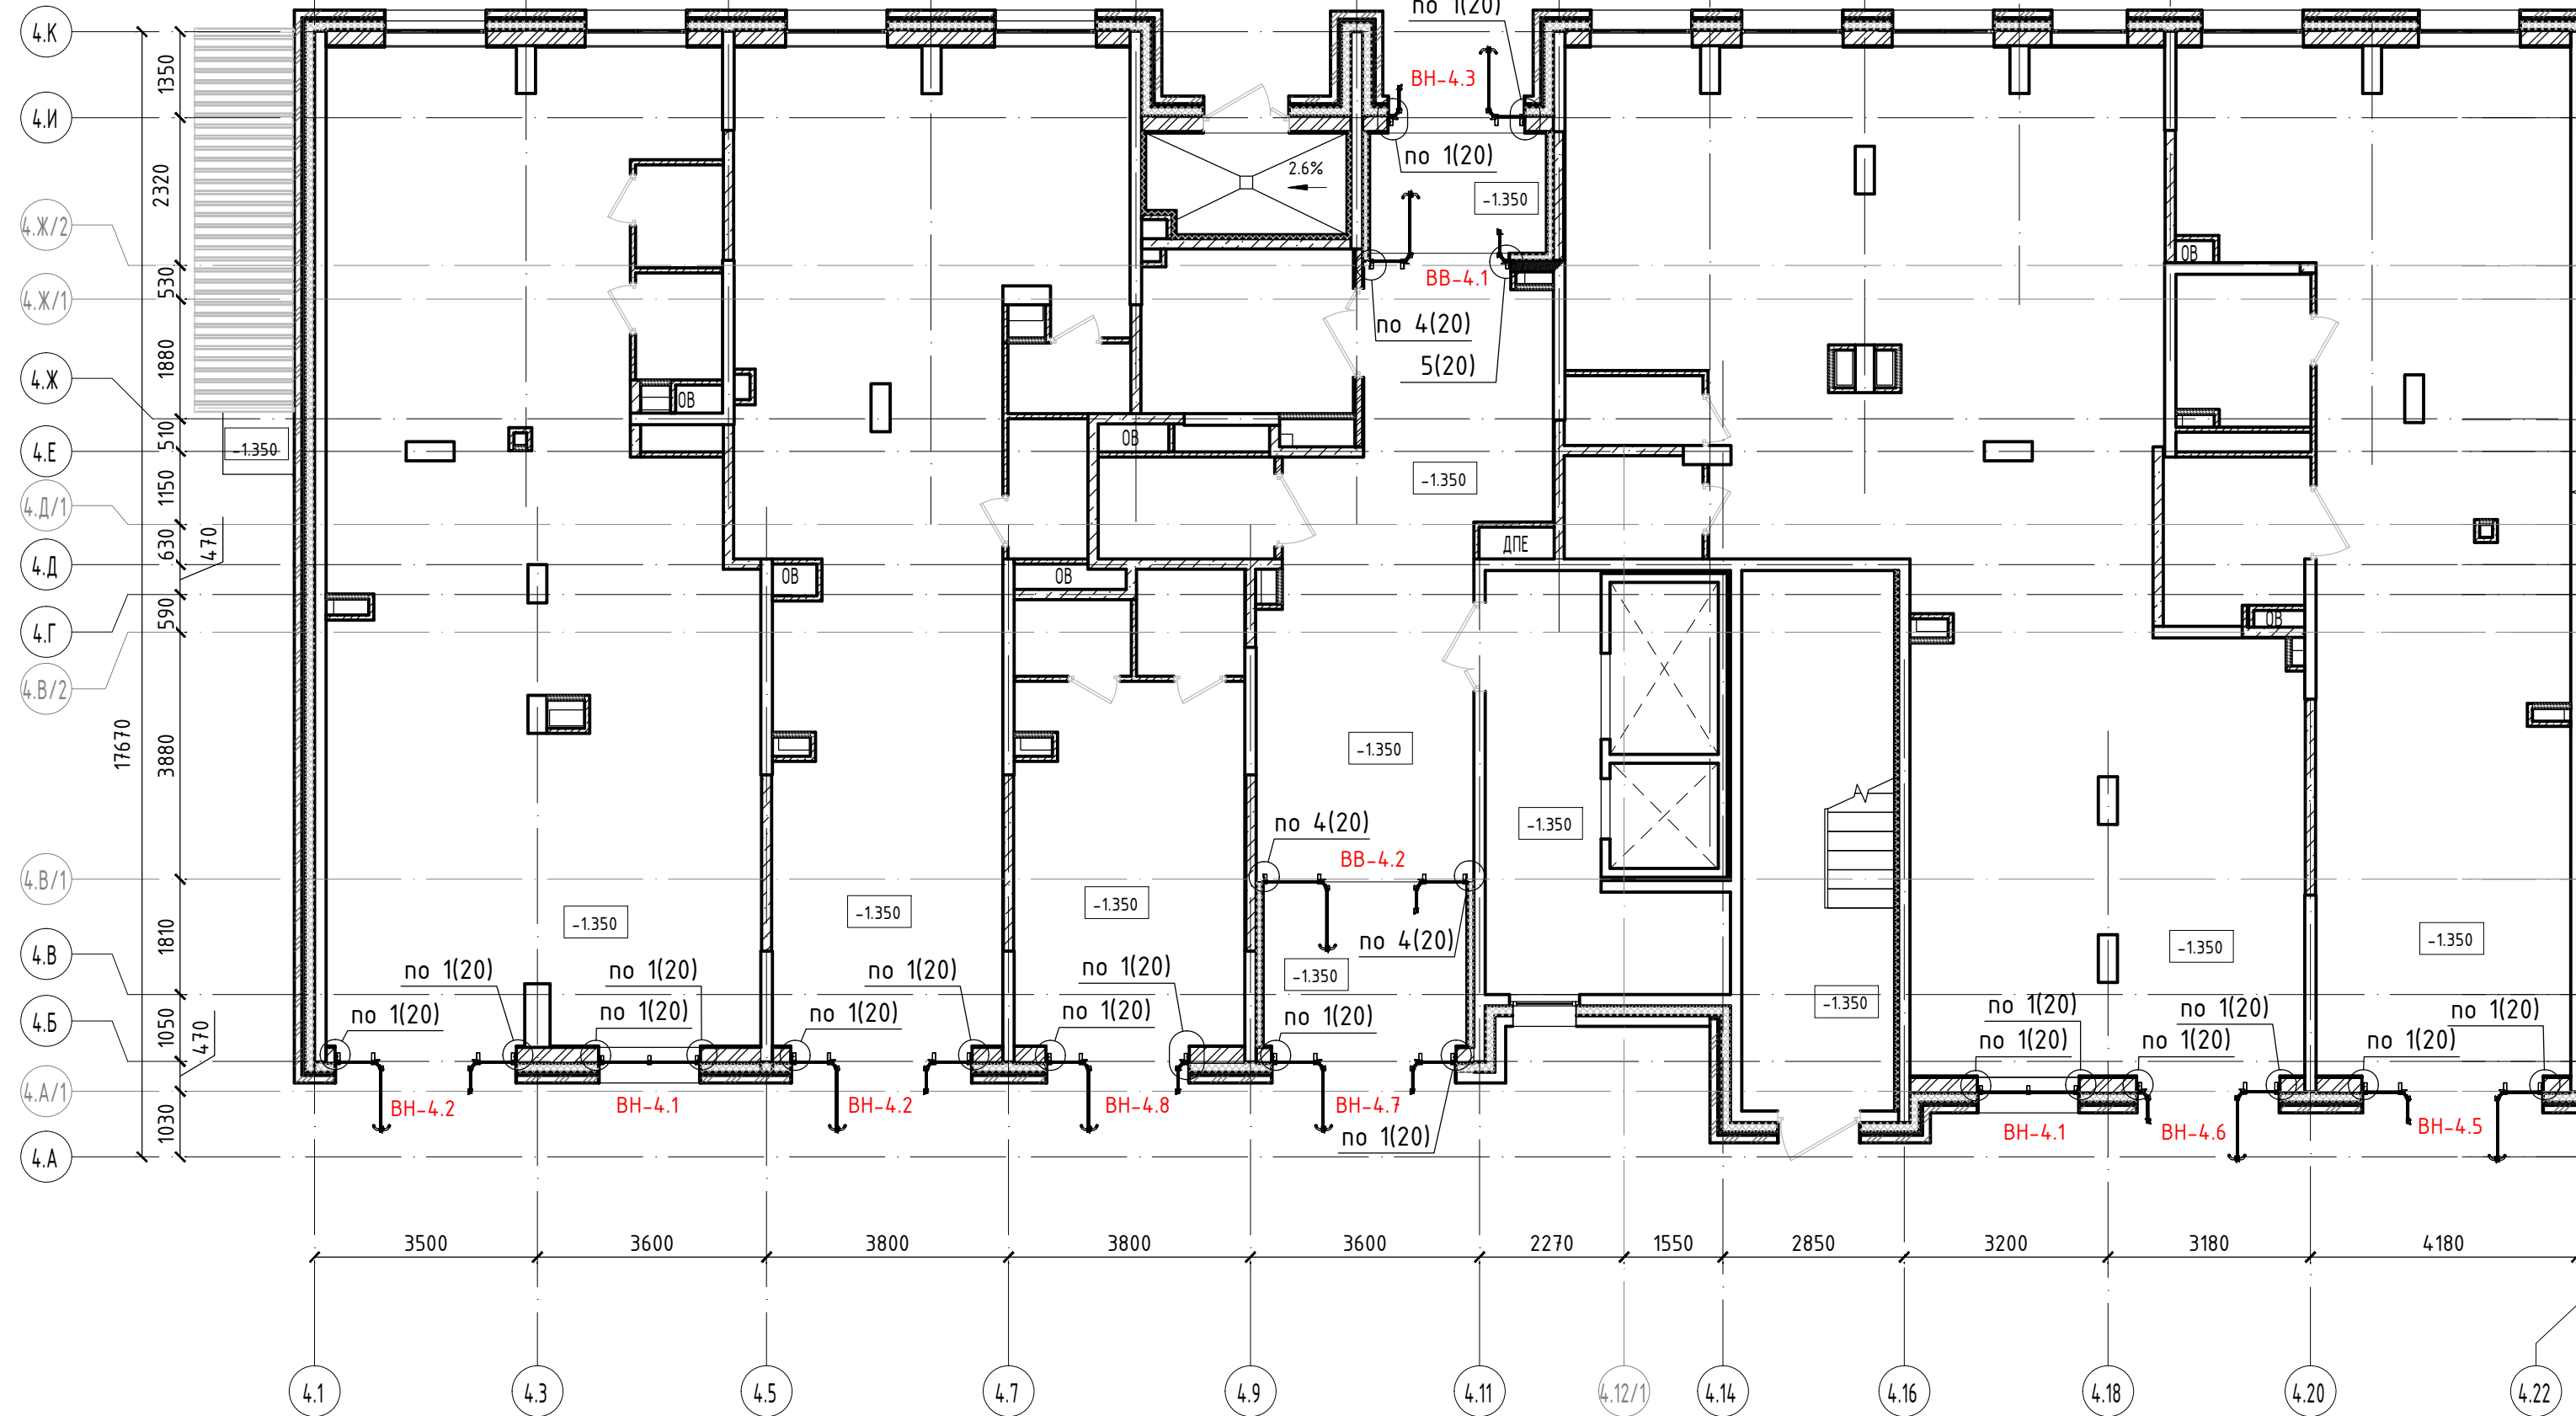


Схема расположения секций

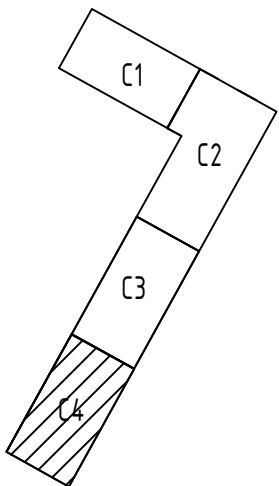

Примечание

1. Общие данные смотри лист 2.
2. Спецификацию свотопрозрачных конструкций смотри лист 25.


						04-2026/Т-104-КМ				
						"Многоквартирный жилой дом со встроенными помещениями" по адресу: Ленинградская область, Всеволожский район, дер. Новосаратовка, кад. №47:07:0605001:1175 (участок 16 по ППТ)				
Изм.	Кол.	Лист	№ док.	Подпись	Дата					
Разработал	Степочкин				06.2026	Многоквартирный жилой дом со встроенными помещениями		Стадия	Лист	Листов
Проверил	Баркалов				06.2026			Р	8	
Н.контр.	Баркалов				06.2026	План 1 этажа. Секция 4		ГК "Технология"		

Согласовано:


10.06.2026 г.

Инв. № подл. Подпись и дата Взам. инв. №


Витраж ВН-1.1 (1 шт.)

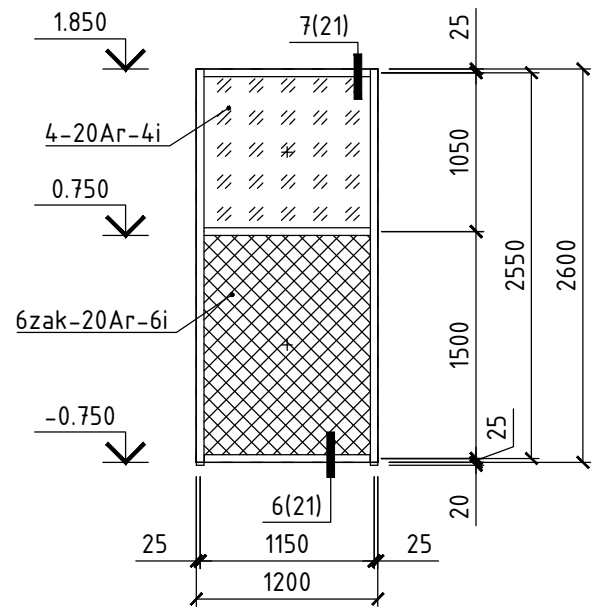

Витраж ВН-1.3 (1 шт.)

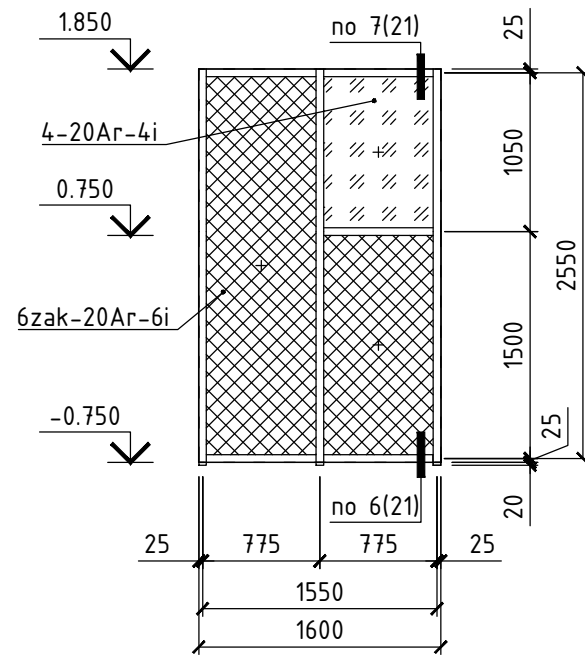

Витраж ВН-1.2 (1 шт.)

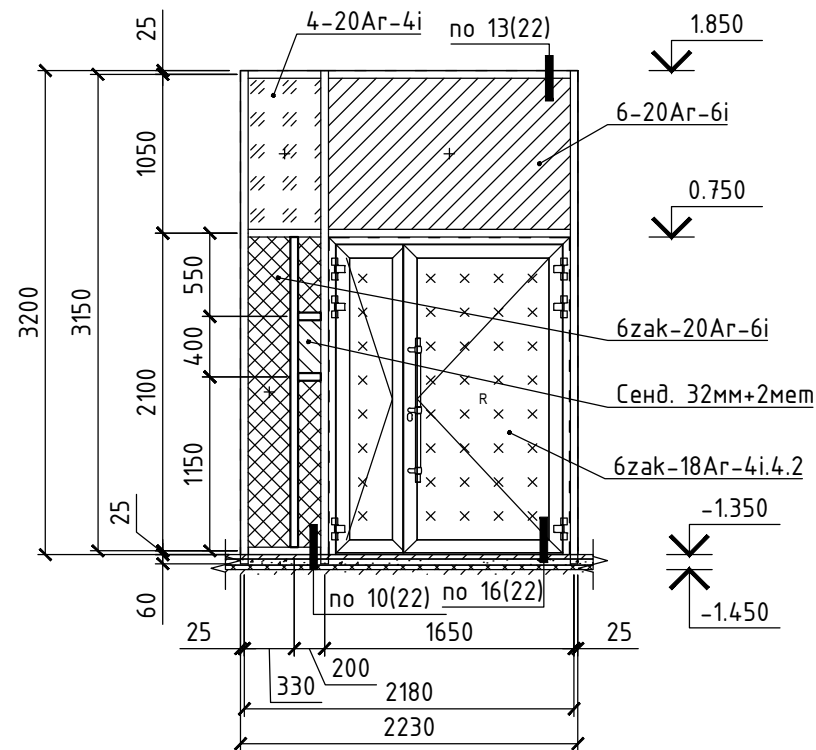

Примечание


- Общие данные смотри лист 2.
- Общие указания смотри лист 3.
- Спецификацию светопрозрачных конструкций смотри лист 25.
- Узлы смотри лист 20-23.
- За отметку 0.000 на фасаде принят уровень чистого пола 1 этажа.
- Каркасы витражей фасадная система TFS 50, дверная серия с терморазрывом TDS 65.
- Вид с фасада здания.
- Фактические размеры конструкций могут отличаться после выполнения геодезической съёмки.
- Покрывтие профилей порошковая окраска RAL 7024.

Ведомость заполнений


Наименование	УГО
4-20Ar-4i Стеклопакет 1-но камерный энергосберегающий, без солнцезащитного покрытия	/// /// /// ///
6zak-18Ar-4i.4.2 Стеклопакет 1-но камерный с закалённым стеклом снаружи, внутри со стеклом триплекс (8 мм) с ударопрочной плёнкой. Класс безопасности SM4	< x x x x > < x x x x > < x x x x > < x x x x >
6zak-20Ar-6i Стеклопакет 1-но камерный энергосберегающий с закалённым стеклом с одной стороны, без солнцезащитного покрытия	/// /// /// ///
6-20Ar-6i Стеклопакет 1-но камерный энергосберегающий, без солнцезащитного покрытия	/// /// /// ///
Сенд. 32мм+2мет Сендвич-панель RAL-7024	/// /// /// ///

						04-2026/Т-104-КМ			
						"Многоквартирный жилой дом со встроенными помещениями" по адресу: Ленинградская область, Всеволожский район, дер. Новосаратовка, кад. №47:07:0605001:1175 (участок 16 по ППТ)			
Изм.	Кол.	Лист	№ док.	Подпись	Дата	Многоквартирный жилой дом со встроенными помещениями	Стадия	Лист	Листов
Разработал	Степочкин				06.2026		Р	9	
Проверил	Баркалов				06.2026				
Н.контр.	Баркалов				06.2026	ВН-1.1.ВН-1.2.ВН1.3		ГК "Технология"	


Витраж ВН-2.1 (1 шт.)

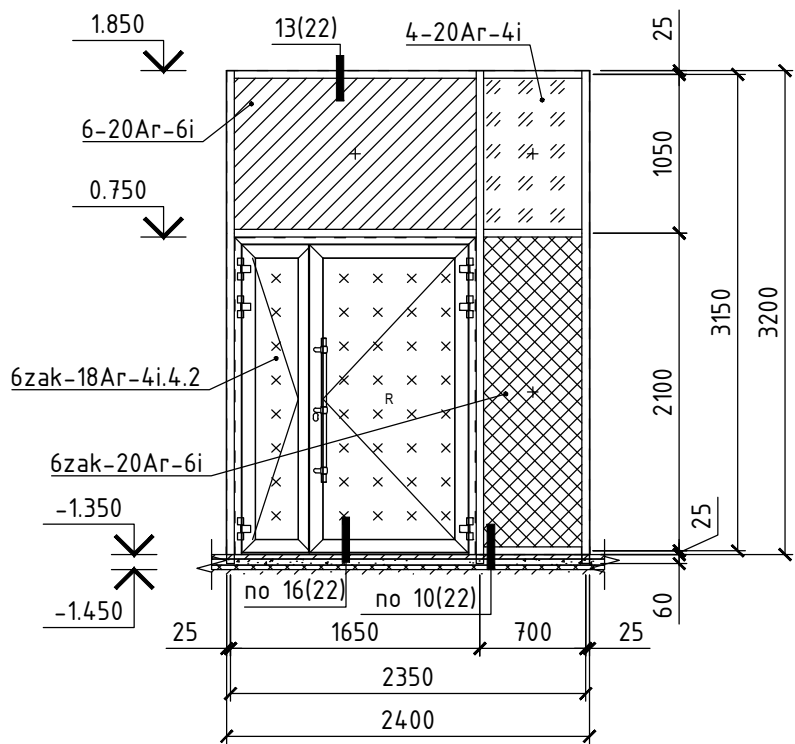

Витраж ВН-2.2 (1 шт.)

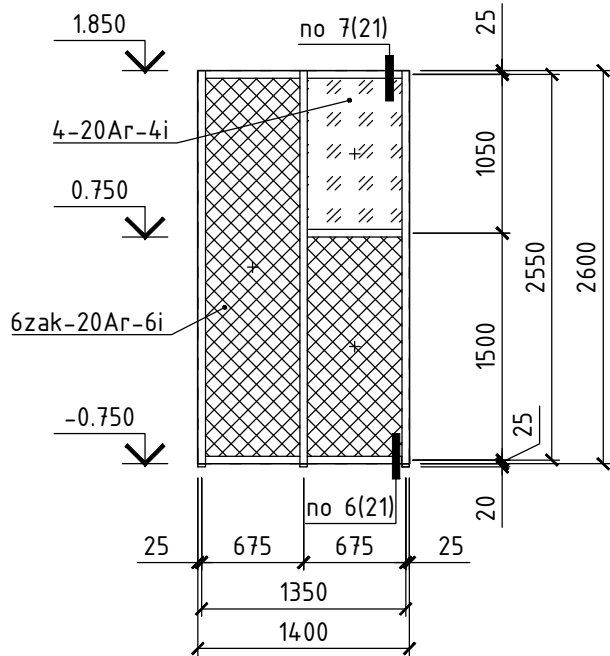

Витраж ВН-2.3 (1 шт.)
Козырёк

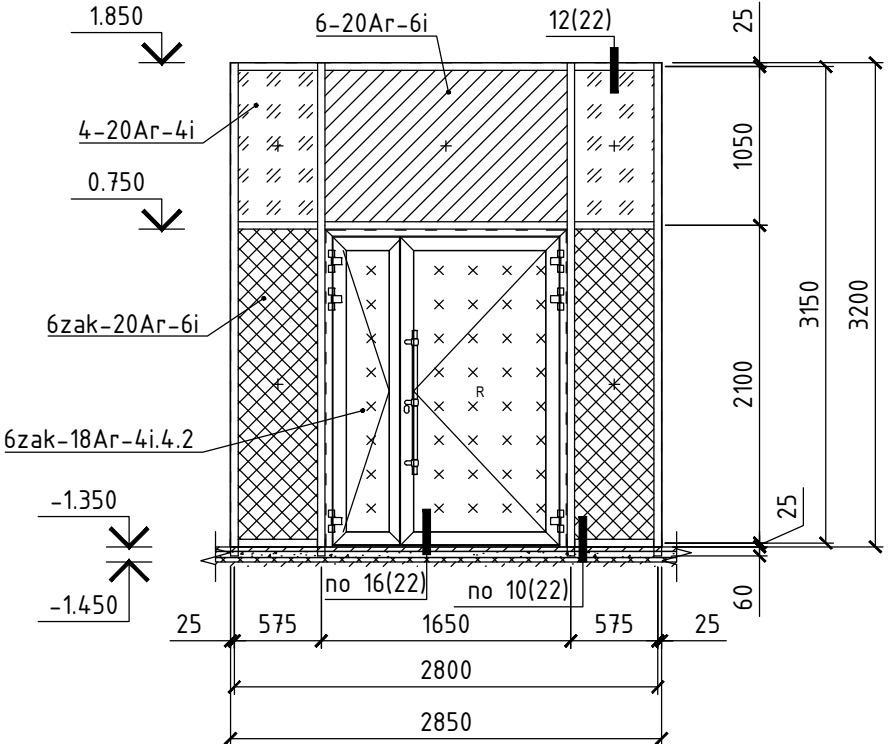

Примечание


- Общие данные смотри лист 2.
- Общие указания смотри лист 3.
- Спецификацию светопрозрачных конструкций смотри лист 25.
- Узлы смотри лист 20-23.
- За отметку 0.000 на фасаде принят уровень чистого пола 1 этажа.
- Каркасы витражей фасадная система TFS 50, дверная серия с терморазрывом TDS 65.
- Вид с фасада здания.
- Фактические размеры конструкций могут отличаться после выполнения геодезической съёмки.
- Покраска профилей порошковая окраска RAL 7024.

Ведомость заполнений


Наименование	УГО
4-20Ar-4i Стеклопакет 1-но камерный энергосберегающий, без солнцезащитного покрытия	/// /// ///
6zak-18Ar-4i.4.2 Стеклопакет 1-но камерный с закалённым стеклом снаружи, внутри со стеклом триплекс (8 мм) с ударопрочной плёнкой. Класс безопасности SM4	< x x x x >
6zak-20Ar-6i Стеклопакет 1-но камерный энергосберегающий с закалённым стеклом с одной стороны, без солнцезащитного покрытия	/// /// ///
6-20Ar-6i Стеклопакет 1-но камерный энергосберегающий, без солнцезащитного покрытия	/// /// ///

						04-2026/Т-104-КМ			
						"Многоквартирный жилой дом со встроенными помещениями" по адресу: Ленинградская область, Всеволожский район, дер. Новосаратовка, кад. №47:07:0605001:1175 (участок 16 по ППТ)			
Изм.	Кол.	Лист	№ док.	Подпись	Дата	Многоквартирный жилой дом со встроенными помещениями	Стадия	Лист	Листов
Разработал	Степочкин				06.2026		Р	10	
Проверил	Баркалов				06.2026				
Н.контр.	Баркалов				06.2026	ВН-2.1.ВН-2.2.ВН2.3		ГК "Технология"	


Витраж ВН-2.7 (1 шт.)

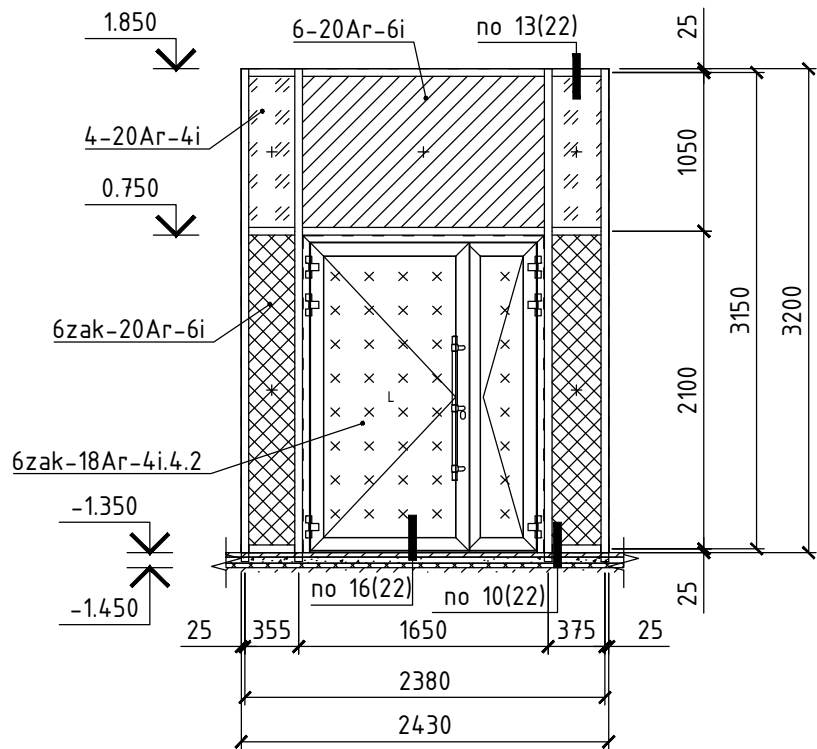

Витраж ВН-3.1 (1 шт.)

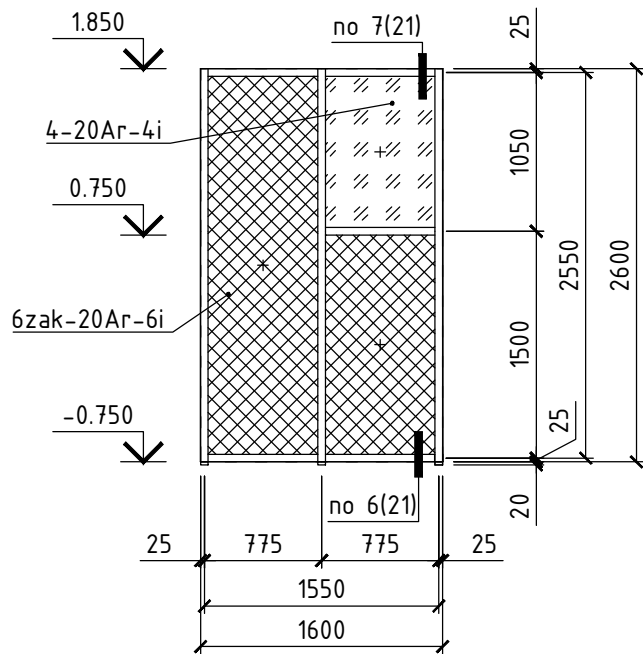

Витраж ВН-3.2 (1 шт.)

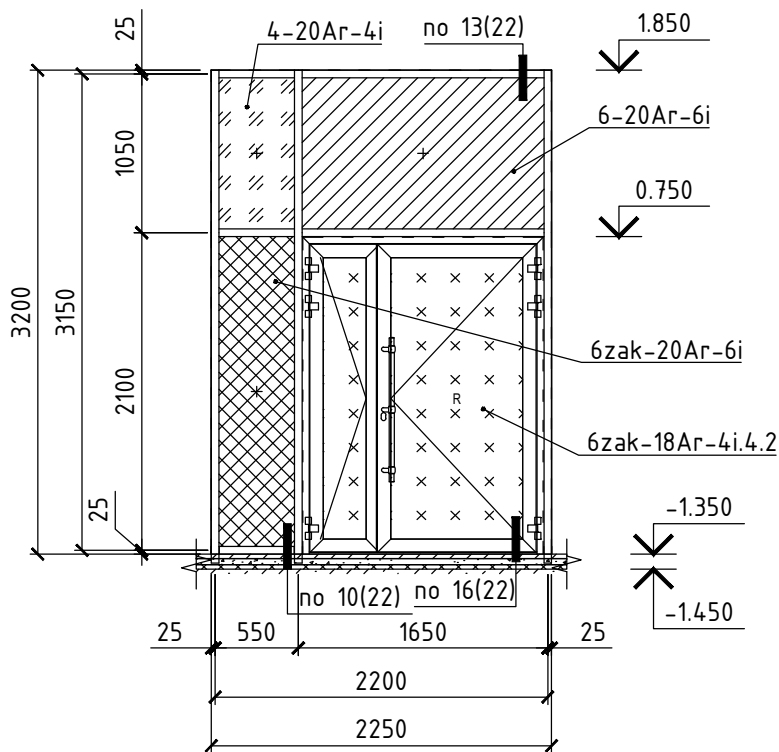

Примечание

- Общие данные смотри лист 2.
- Общие указания смотри лист 3.
- Спецификацию светопрозрачных конструкций смотри лист 25.
- Узлы смотри лист 20-23.
- За отметку 0.000 на фасаде принят уровень чистого пола 1 этажа.
- Каркасы витражей фасадная система TFS 50, дверная серия с терморазрывом TDS 65.
- Вид с фасада здания.
- Фактические размеры конструкций могут отличаться после выполнения геодезической съёмки.
- Покрывтие профилей порошковая окраска RAL 7024.


Ведомость заполнений

Наименование	УГО
4-20Ar-4i Стеклопакет 1-но камерный энергосберегающий, без солнцезащитного покрытия	/// /// /// ///
6zak-18Ar-4i.4.2 Стеклопакет 1-но камерный с закалённым стеклом снаружи, внутри со стеклом триплекс (8 мм) с ударопрочной плёнкой. Класс безопасности SM4	< x x x x > < x x x x > < x x x x > < x x x x >
6zak-20Ar-6i Стеклопакет 1-но камерный энергосберегающий с закалённым стеклом с одной стороны, без солнцезащитного покрытия	/// /// /// ///
6-20Ar-6i Стеклопакет 1-но камерный энергосберегающий, без солнцезащитного покрытия	/// /// /// ///


						04-2026/Т-104-КМ			
						"Многоквартирный жилой дом со встроенными помещениями" по адресу: Ленинградская область, Всеволожский район, дер. Новосаратовка, кад. №47:07:0605001:1175 (участок 16 по ППТ)			
Изм.	Кол.	Лист	№ док.	Подпись	Дата	Многоквартирный жилой дом со встроенными помещениями	Стадия	Лист	Листов
Разработал	Степочкин				06.2026		Р	12	
Проверил	Баркалов				06.2026				
Н.контр.	Баркалов				06.2026	ВН-2.7.ВН-3.1.ВН-3.2		ГК "Технология"	

Витраж ВН-3.3 (1 шм.)

Козырёк

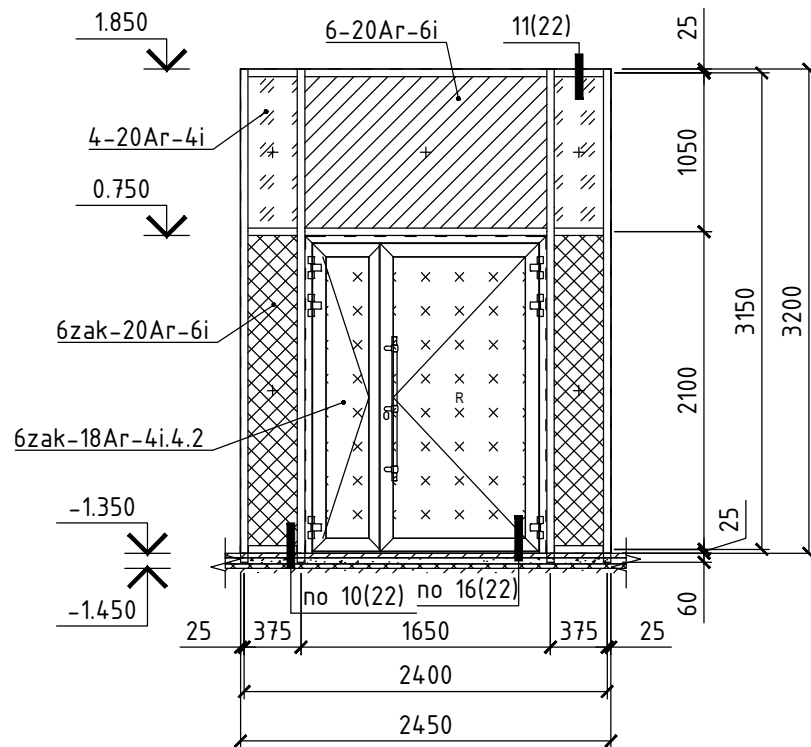


Витраж ВН-3.4 (1 шм.)

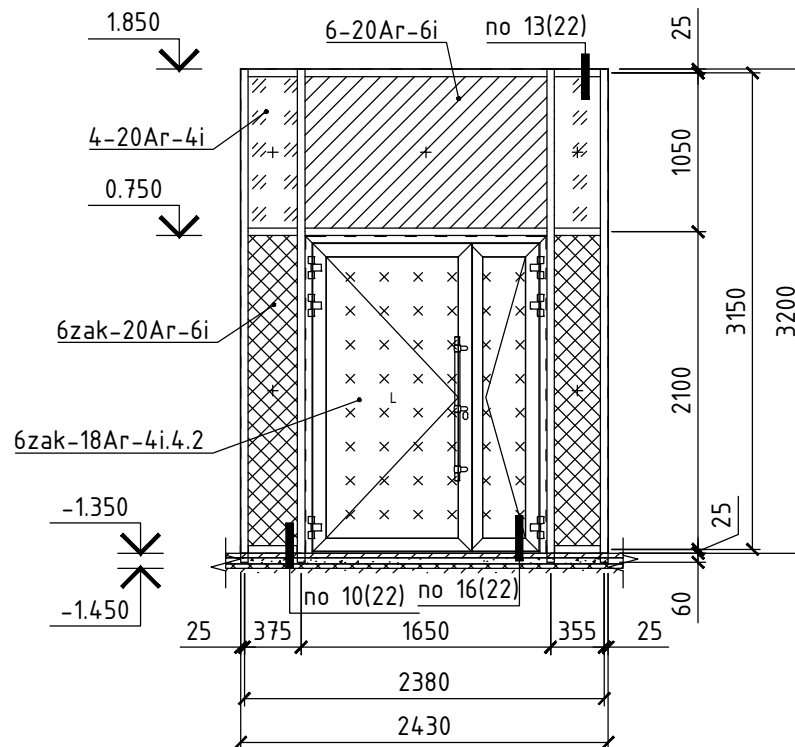

Ведомость заполнений

Наименование	УГО
4-20Ar-4i Стеклопакет 1-но камерный энергосберегающий, без солнцезащитного покрытия	/// /// /// ///
6zak-18Ar-4i.4.2 Стеклопакет 1-но камерный с закалённым стеклом снаружи, внутри со стеклом триплекс (8 мм) с ударопрочной плёнкой. Класс безопасности SM4	< x x x x > < x x x x > < x x x x > < x x x x >
6zak-20Ar-6i Стеклопакет 1-но камерный энергосберегающий с закалённым стеклом с одной стороны, без солнцезащитного покрытия	
6-20Ar-6i Стеклопакет 1-но камерный энергосберегающий, без солнцезащитного покрытия	

Витраж ВН-3.5 (1 шм.)

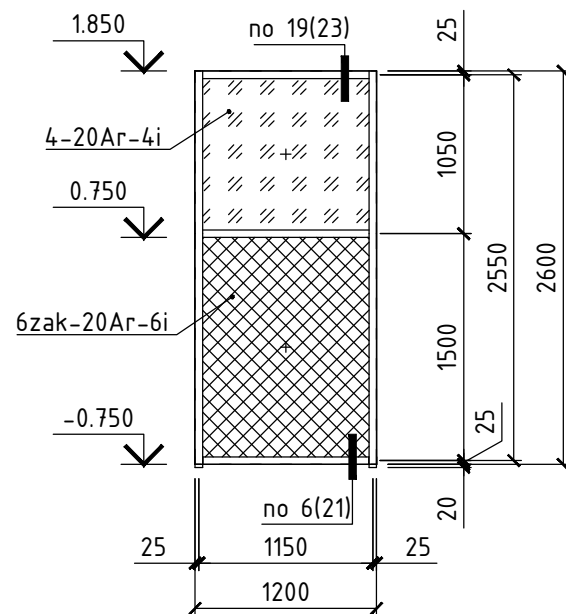


Примечание


- Общие данные смотри лист 2.
- Общие указания смотри лист 3.
- Спецификацию светопрозрачных конструкций смотри лист 25.
- Узлы смотри лист 20-23.
- За отметку 0.000 на фасаде принят уровень чистого пола 1 этажа.
- Каркасы витражей фасадная система TFS 50, дверная серия с терморазрывом TDS 65.
- Вид с фасада здания.
- Фактические размеры конструкций могут отличаться после выполнения геодезической съёмки.
- Покрытие профилей порошковая окраска RAL 7024.

						04-2026/Т-104-КМ			
						"Многоквартирный жилой дом со встроенными помещениями" по адресу: Ленинградская область, Всеволожский район, дер. Новосаратовка, кад. №47:07:0605001:1175 (участок 16 по ППТ)			
Изм.	Кол.	Лист	№ док.	Подпись	Дата	Многоквартирный жилой дом со встроенными помещениями	Стадия	Лист	Листов
Разработал	Степочкин				06.2026		Р	13	
Проверил	Баркалов				06.2026				
Н.контр.	Баркалов				06.2026	ВН-3.3.ВН-3.4.ВН-3.5		ГК "Технология"	

Витраж ВН-3.6 (2 шт.)
Козырёк

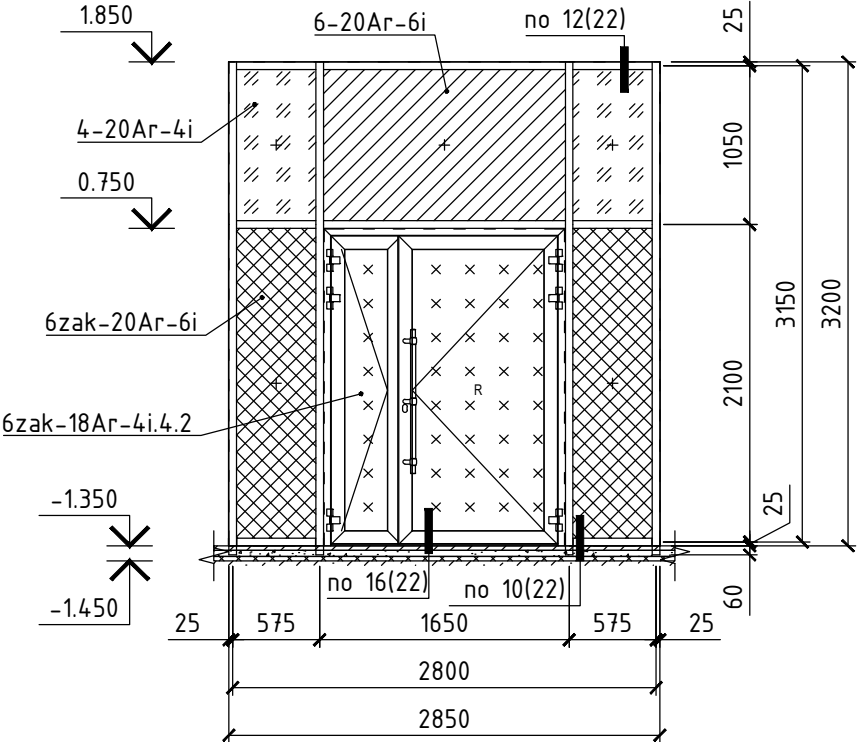


Витраж ВН-3.7 (1 шт.)

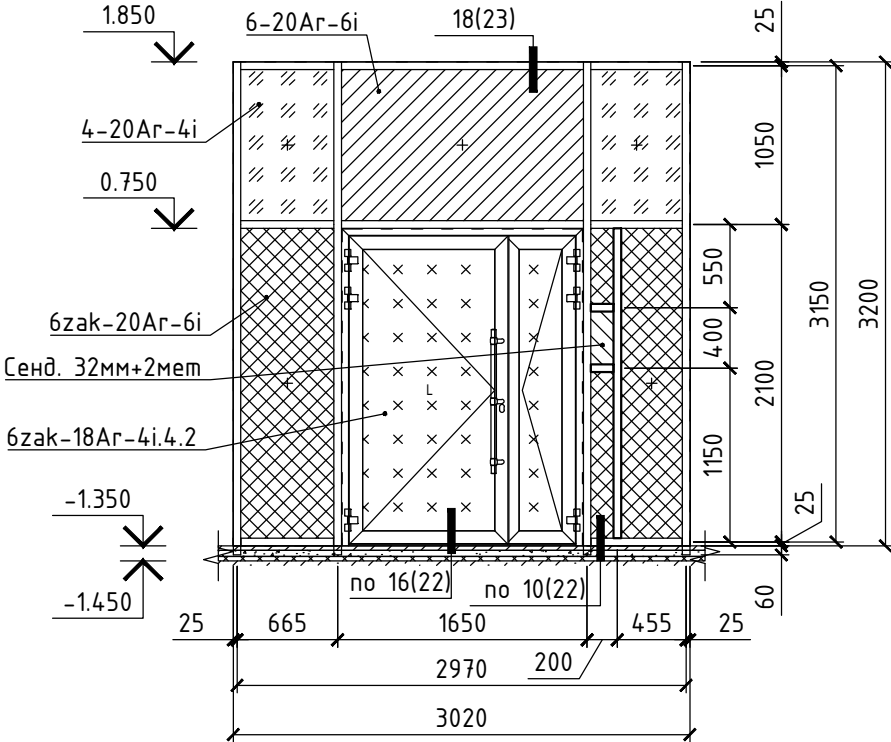

Ведомость заполнений

Наименование	УГО
4-20Ar-4i Стеклопакет 1-но камерный энергосберегающий, без солнцезащитного покрытия	/// /// /// /// /// /// /// /// /// /// /// ///
6zak-18Ar-4i.4.2 Стеклопакет 1-но камерный с закалённым стеклом снаружи, внутри со стеклом триплекс (8 мм) с ударопрочной плёнкой. Класс безопасности SM4	< x x x > < x x x > < x x x > < x x x >
6zak-20Ar-6i Стеклопакет 1-но камерный энергосберегающий с закалённым стеклом с одной стороны, без солнцезащитного покрытия	/// /// /// /// /// /// /// /// /// /// /// ///
6-20Ar-6i Стеклопакет 1-но камерный энергосберегающий, без солнцезащитного покрытия	/// /// /// /// /// /// /// /// /// /// /// ///
Сенд. 32мм+2мет Сендвич-панель RAL-7024	/// /// /// /// /// /// /// /// /// /// /// ///

Витраж ВН-3.8 (1 шт.)

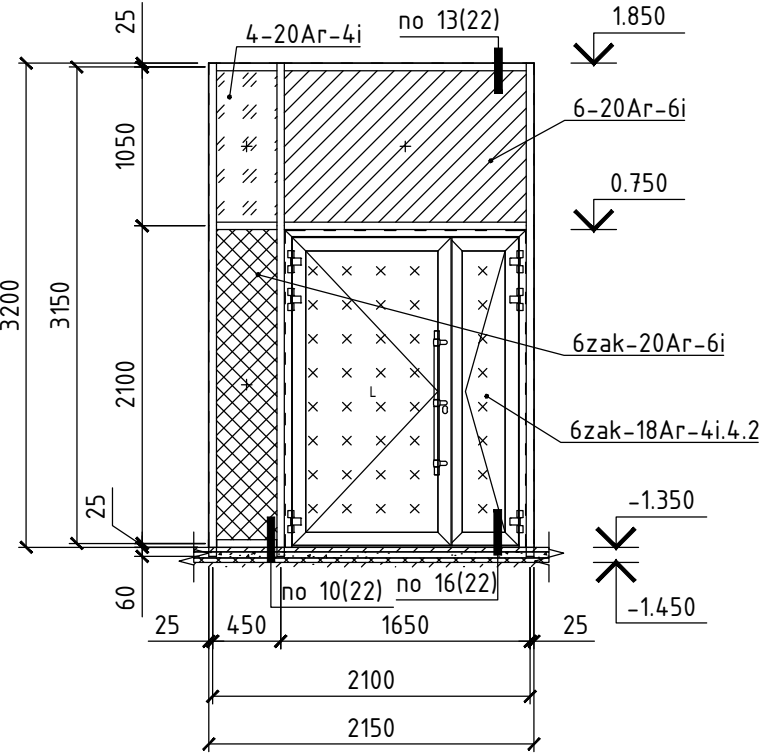


Примечание

- Общие данные смотри лист 2.
- Общие указания смотри лист 3.
- Спецификацию светопрозрачных конструкций смотри лист 25.
- Узлы смотри лист 20-23.
- За отметку 0.000 на фасаде принят уровень чистого пола 1 этажа.
- Каркасы витражей фасадная система TFS 50, дверная серия с терморазрывом TDS 65.
- Вид с фасада здания.
- Фактические размеры конструкций могут отличаться после выполнения геодезической съёмки.
- Покрытие профилей порошковая окраска RAL 7024.


						04-2026/Т-104-КМ		
						"Многоквартирный жилой дом со встроенными помещениями" по адресу: Ленинградская область, Всеволожский район, дер. Новосаратовка, кад. №47:07:0605001:1175 (участок 16 по ППТ)		
Изм.	Кол.	Лист	№ док.	Подпись	Дата	Многоквартирный жилой дом со встроенными помещениями	Стадия	Лист
Разработал	Степочкин				06.2026		Р	14
Проверил	Баркалов				06.2026			
Н.контр.	Баркалов				06.2026	ВН-3.6.ВН-3.7.ВН-3.8		ГК "Технология"

Витраж ВН-4.3 (1 шт.)

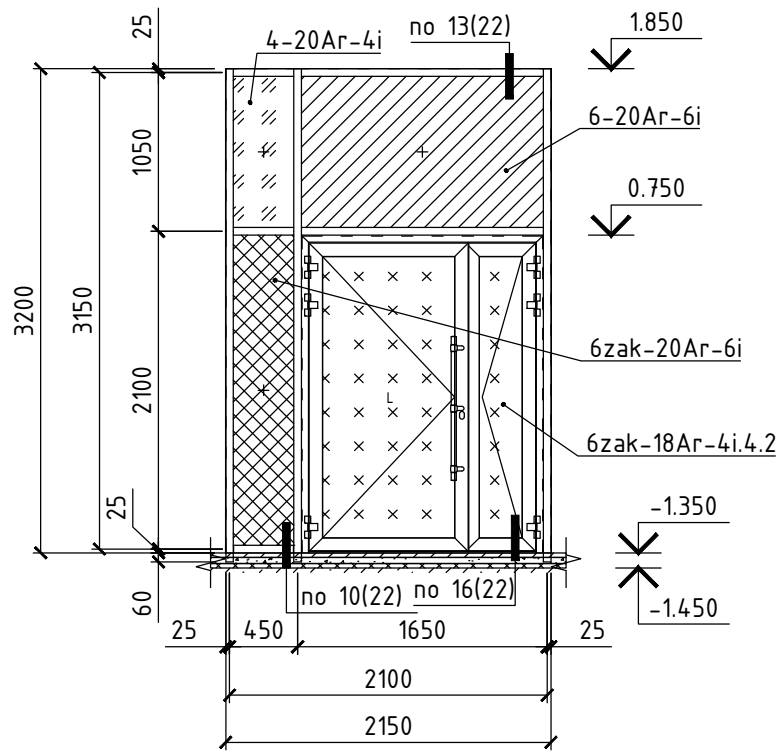


Витраж ВН-4.5 (1 шт.)

Козырёк

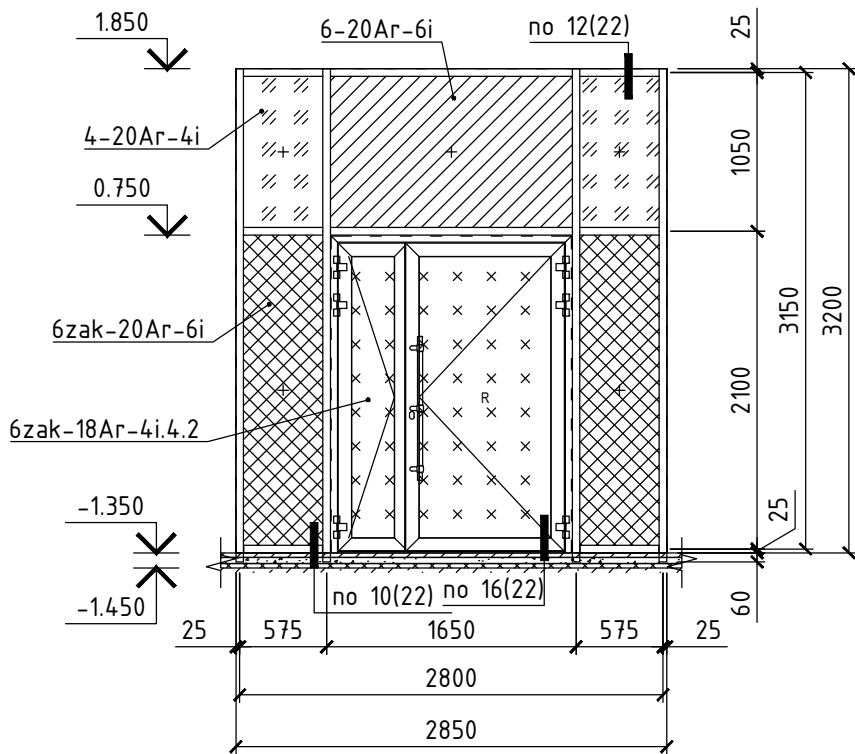

Витраж ВН-4.6 (1 шт.)

Козырёк

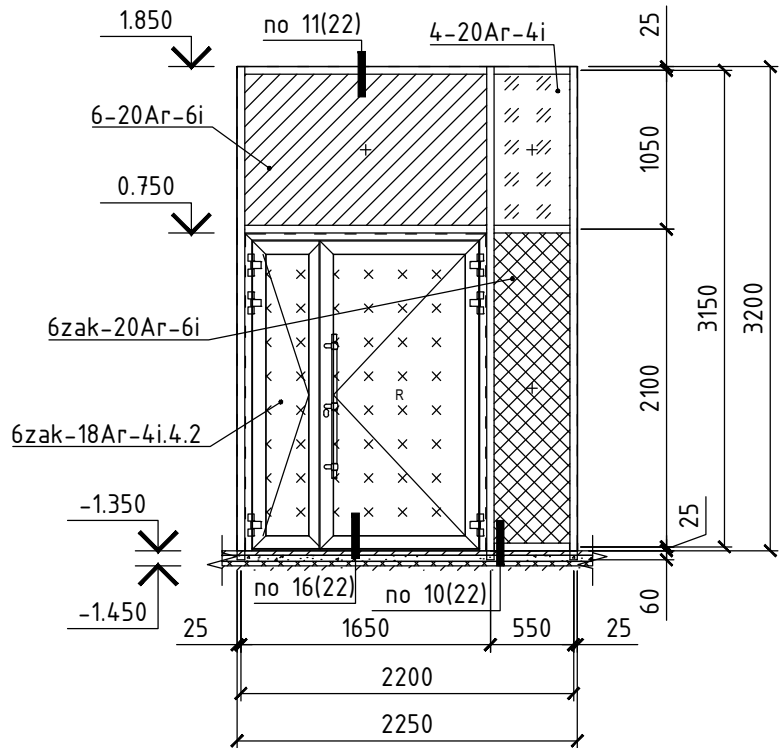

Примечание

- Общие данные смотри лист 2.
- Общие указания смотри лист 3.
- Спецификацию светопрозрачных конструкций смотри лист 25.
- Узлы смотри лист 20-23.
- За отметку 0.000 на фасаде принят уровень чистого пола 1 этажа.
- Каркасы витражей фасадная система TFS 50, дверная серия с терморазрывом TDS 65.
- Вид с фасада здания.
- Фактические размеры конструкций могут отличаться после выполнения геодезической съёмки.
- Покрывтие профилей порошковая окраска RAL 7024.

Ведомость заполнений

Наименование	УГО
4-20Ar-4i Стеклопакет 1-но камерный энергосберегающий, без солнцезащитного покрытия	/// /// /// ///
6zak-18Ar-4i.4.2 Стеклопакет 1-но камерный с закалённым стеклом снаружи, внутри со стеклом триплекс (8 мм) с ударопрочной плёнкой. Класс безопасности SM4	< x x x x > < x x x x > < x x x x > < x x x x >
6zak-20Ar-6i Стеклопакет 1-но камерный энергосберегающий с закалённым стеклом с одной стороны, без солнцезащитного покрытия	/// /// /// ///
6-20Ar-6i Стеклопакет 1-но камерный энергосберегающий, без солнцезащитного покрытия	/// /// /// ///


						04-2026/Т-104-КМ			
						"Многоквартирный жилой дом со встроенными помещениями" по адресу: Ленинградская область, Всеволожский район, дер. Новосаратовка, кад. №47:07:0605001:1175 (участок 16 по ППТ)			
Изм.	Кол.	Лист	№ док.	Подпись	Дата	Многоквартирный жилой дом со встроенными помещениями	Стадия	Лист	Листов
Разработал		Степочкин			06.2026		Р	16	
Проверил		Баркалов			06.2026				
Н.контр.		Баркалов			06.2026	ВН-4.3.ВН-4.5.ВН-4.6	ГК "Технология"		

Согласовано:


10.06.2026 г.

Инв. № подл. Подпись и дата Взам. инв. №

Витраж ВН-4.7 (1 шт.)

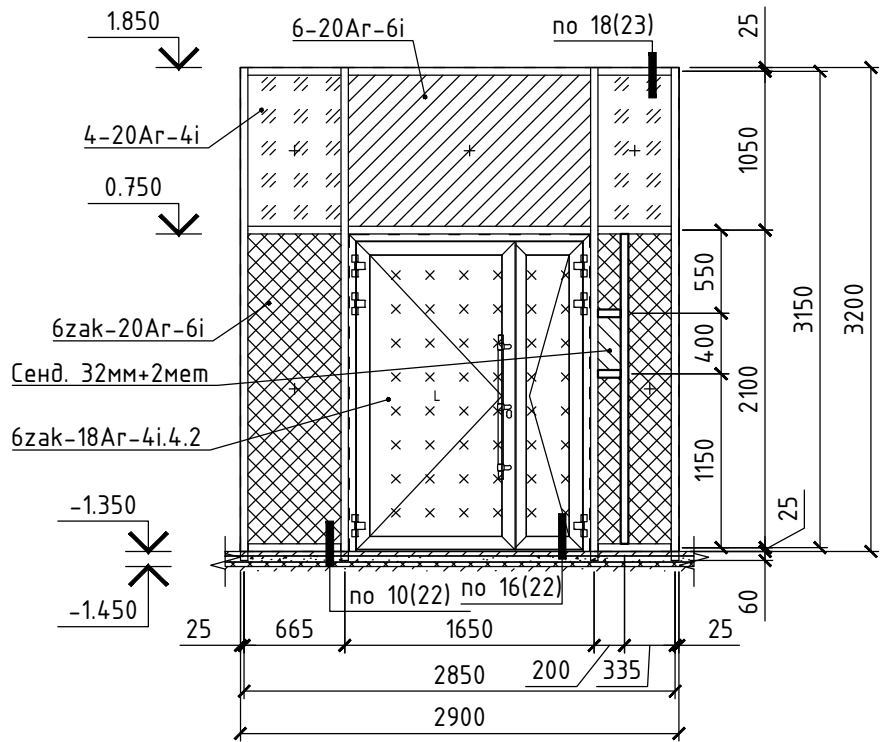

Витраж ВН-4.8 (1 шт.)

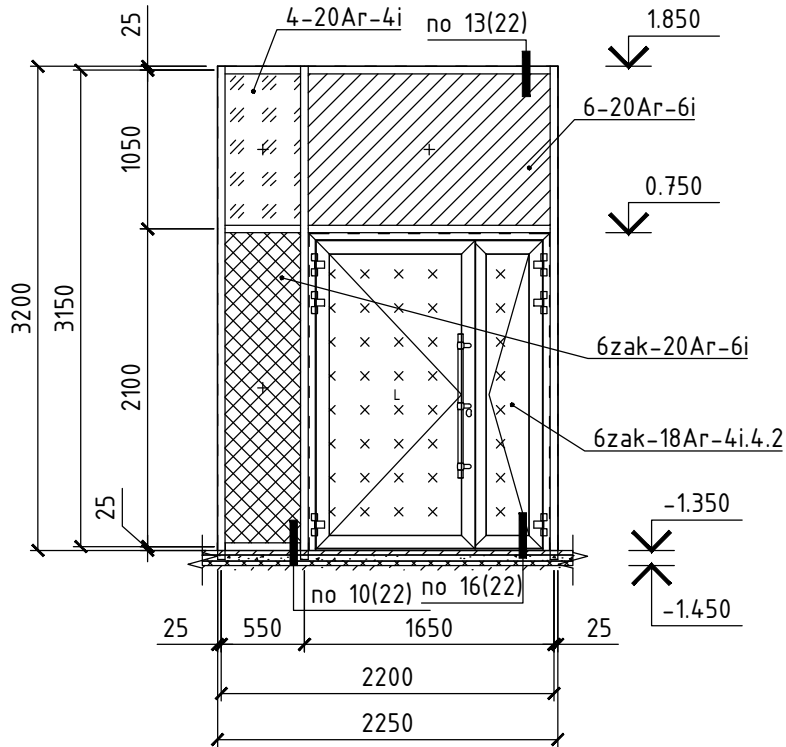

Ведомость заполнений


Наименование	УГО
4-20Ar-4i Стеклопакет 1-но камерный энергосберегающий, без солнцезащитного покрытия	/// /// /// ///
6zak-18Ar-4i.4.2 Стеклопакет 1-но камерный с закалённым стеклом снаружи, внутри со стеклом триплекс (8 мм) с ударопрочной плёнкой. Класс безопасности SM4	< x x x x > < x x x x > < x x x x > < x x x x >
6zak-20Ar-6i Стеклопакет 1-но камерный энергосберегающий с закалённым стеклом с одной стороны, без солнцезащитного покрытия	/// /// /// ///
6-20Ar-6i Стеклопакет 1-но камерный энергосберегающий, без солнцезащитного покрытия	/// /// /// ///
Сенд. 32мм+2мет Сендвич-панель RAL-7024	/// /// /// ///

Примечание


- Общие данные смотри лист 2.
- Общие указания смотри лист 3.
- Спецификацию светопрозрачных конструкций смотри лист 25.
- Узлы смотри лист 20-23.
- За отметку 0.000 на фасаде принят уровень чистого пола 1 этажа.
- Каркасы витражей фасадная система TFS 50, дверная серия с терморазрывом TDS 65.
- Вид с фасада здания.
- Фактические размеры конструкций могут отличаться после выполнения геодезической съёмки.
- Покрытие профилей порошковая окраска RAL 7024.

						04-2026/Т-104-КМ			
						"Многоквартирный жилой дом со встроенными помещениями" по адресу: Ленинградская область, Всеволожский район, дер. Новосаратовка, кад. №47:07:0605001:1175 (участок 16 по ППТ)			
Изм.	Кол.	Лист	№ док.	Подпись	Дата				
						Многоквартирный жилой дом со встроенными помещениями	Стадия	Лист	Листов
Разработал	Степочкин				06.2026		Р	17	
Проверил	Баркалов				06.2026				
Н.контр.	Баркалов				06.2026	ВН-4.7.ВН-4.8	ГК "Технология"		

Витраж ВВ-1.1 (1 шт.)

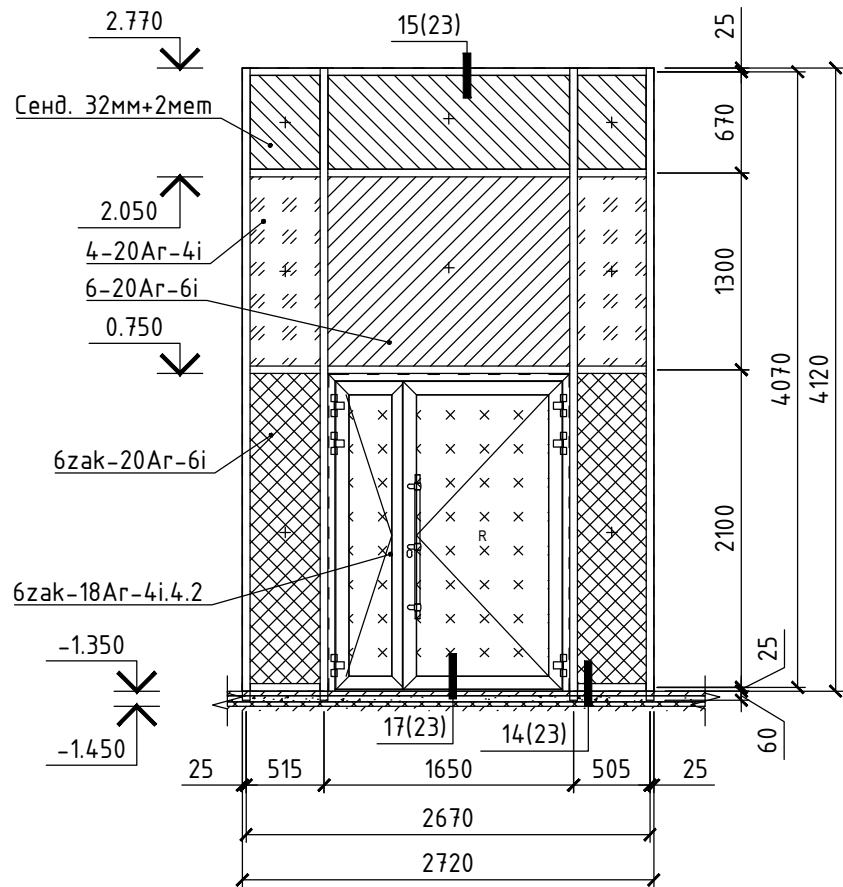


Витраж ВВ-3.1 (1 шт.)

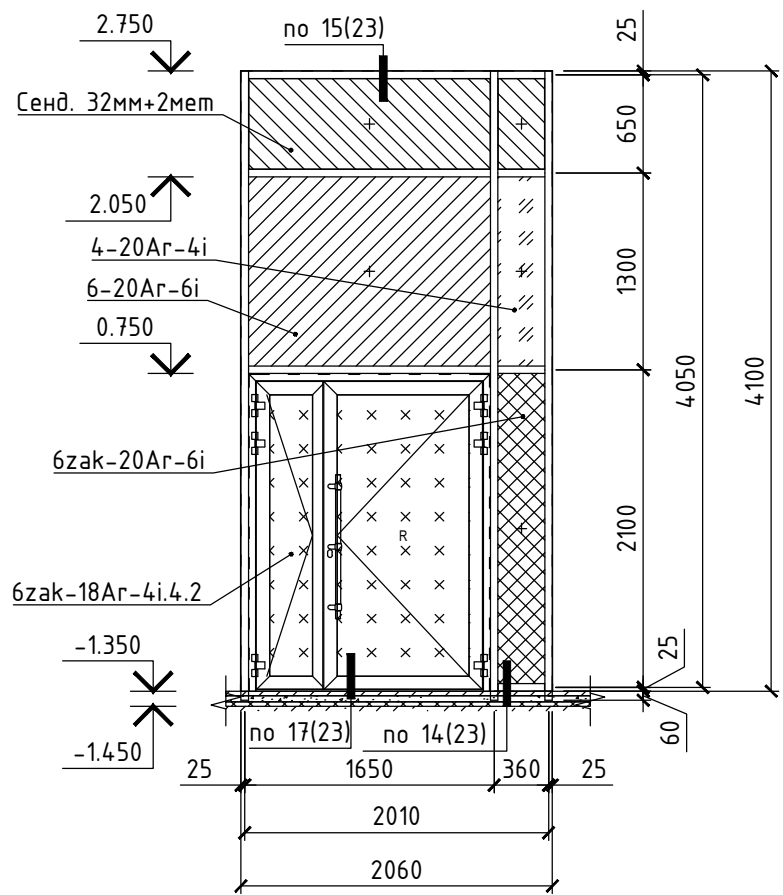

Ведомость заполнений

Наименование	УГО
4-20Ar-4i Стеклопакет 1-но камерный энергосберегающий, без солнцезащитного покрытия	///
6zak-18Ar-4i.4.2 Стеклопакет 1-но камерный с закалённым стеклом снаружи, внутри со стеклом триплекс (8 мм) с ударопрочной плёнкой. Класс безопасности SM4	< x x x >
6zak-20Ar-6i Стеклопакет 1-но камерный энергосберегающий с закалённым стеклом с одной стороны, без солнцезащитного покрытия	///
6-20Ar-6i Стеклопакет 1-но камерный энергосберегающий, без солнцезащитного покрытия	///
6zak-20Ar-6zakRAL7024 Стеклопакет 1-но камерный с закалёнными стёклами, без солнцезащитного покрытия, с обратнокрашенным стеклом RAL-7024 с одной стороны	///
Сенд. 32мм+2мет Сендвич-панель RAL-7024	///

Витраж ВВ-3.2 (1 шт.)

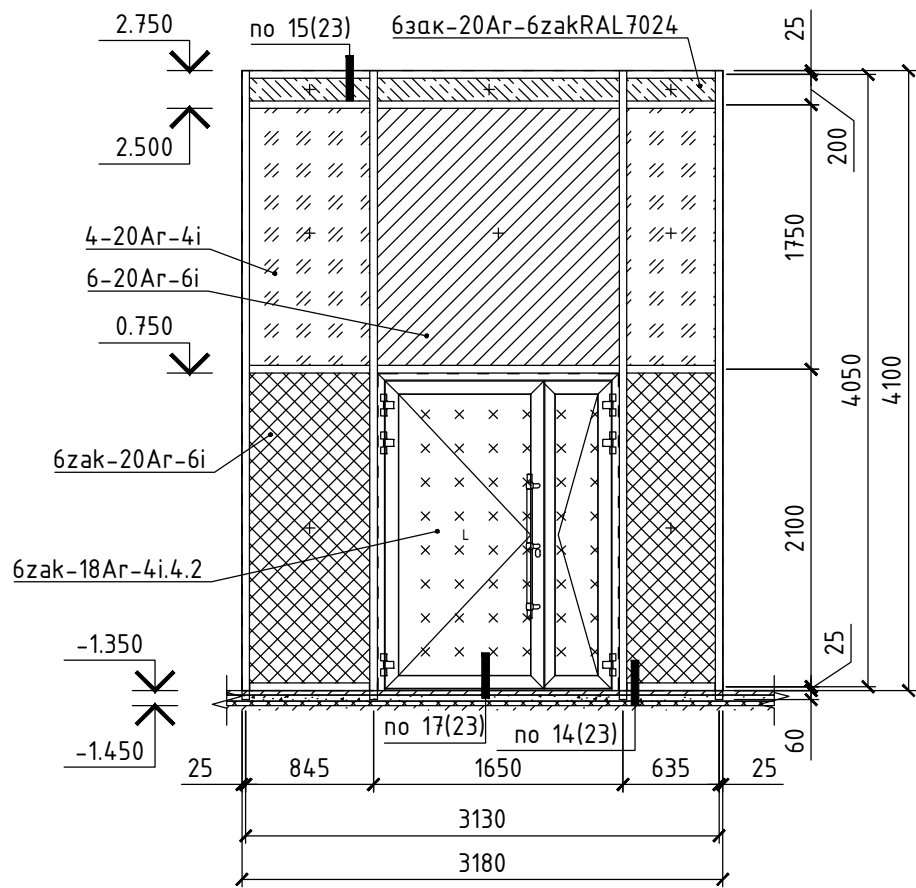

Примечание

- Общие данные смотри лист 2.
- Общие указания смотри лист 3.
- Спецификацию светопрозрачных конструкций смотри лист 25.
- Узлы смотри лист 20-23.
- За отметку 0.000 на фасаде принят уровень чистого пола 1 этажа.
- Каркасы витражей фасадная система TFS 50, дверная серия с терморазрывом TDS 65.
- Вид с фасада здания.
- Фактические размеры конструкций могут отличаться после выполнения геодезической съёмки.
- Покрытие профилей порошковая окраска RAL 7024.


						04-2026/Т-104-КМ		
						"Многоквартирный жилой дом со встроенными помещениями" по адресу: Ленинградская область, Всеволожский район, дер. Новосаратовка, кад. №47:07:0605001:1175 (участок 16 по ППТ)		
Изм.	Кол.	Лист	№ док.	Подпись	Дата	Многоквартирный жилой дом со встроенными помещениями	Стадия	Лист
Разработал	Степочкин				06.2026		Р	18
Проверил	Баркалов				06.2026			
Н.контр.	Баркалов				06.2026	ВВ-1.1.ВВ-3.1.ВВ-3.2		ГК "Технология"

Согласовано:


10.06.2026 г.

Инв. № подл. Подпись и дата Взам. инв. №

Витраж ВВ-4.1 (1 шт.)

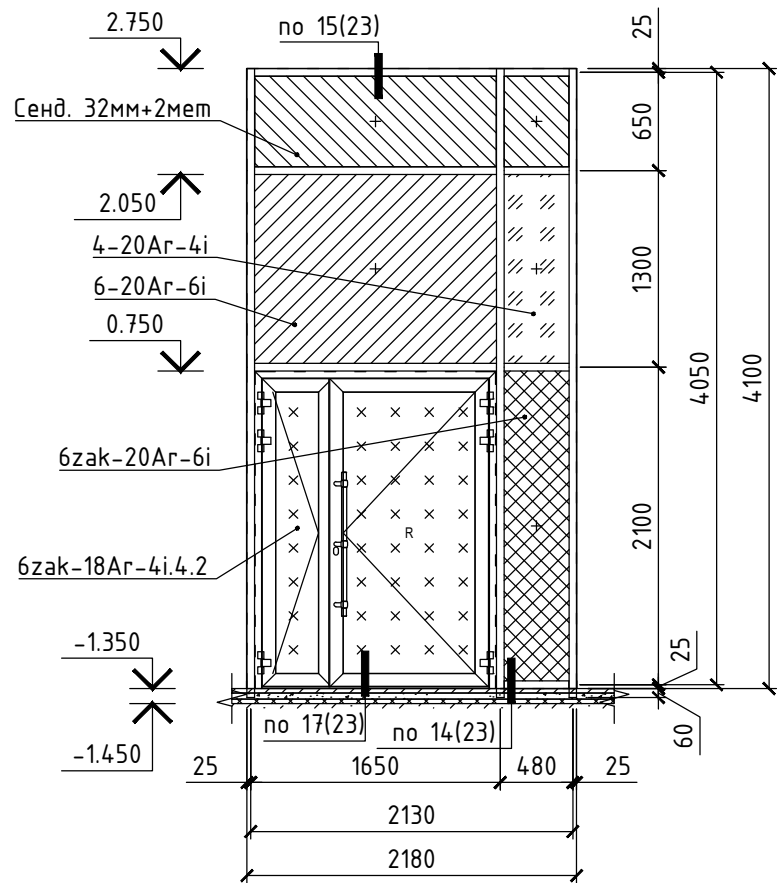

Витраж ВВ-4.2 (1 шт.)

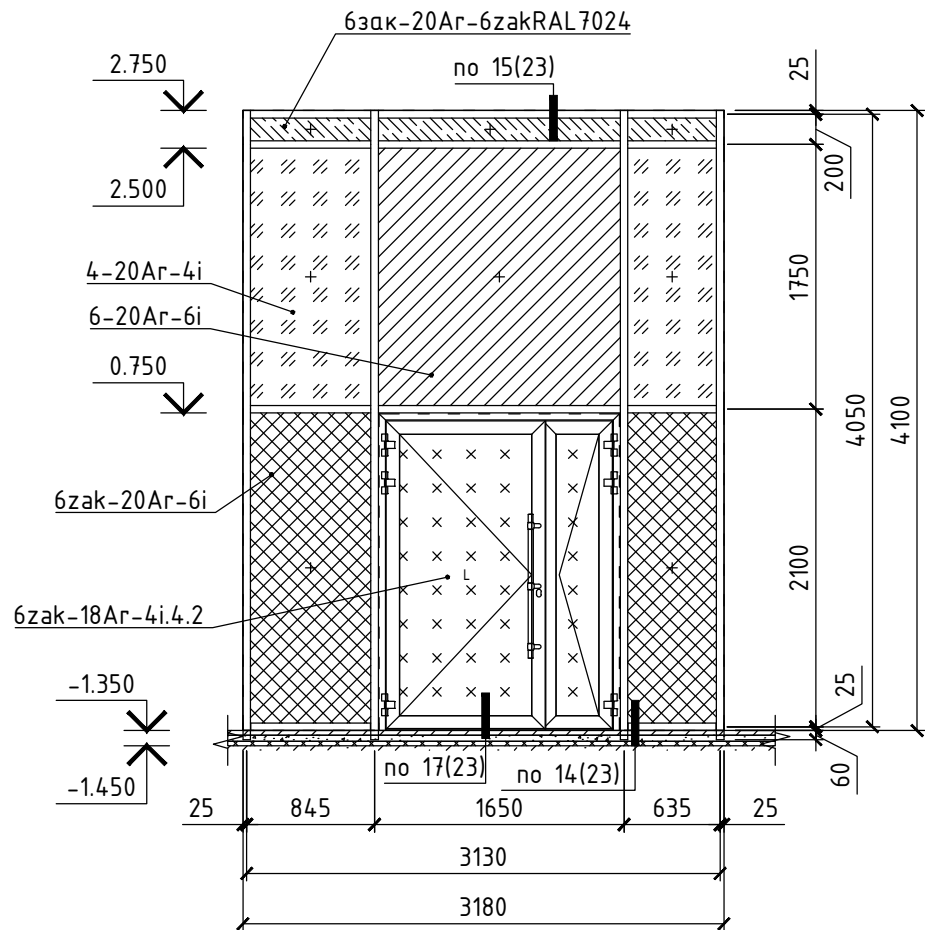

Ведомость заполнений






Наименование	УГО
4-20Ar-4i Стеклопакет 1-но камерный энергосберегающий, без солнцезащитного покрытия	/// /// ///
6zak-18Ar-4i.4.2 Стеклопакет 1-но камерный с закалённым стеклом снаружи, внутри со стеклом триплекс (8 мм) с ударопрочной плёнкой. Класс безопасности SM4	< x x x x >
6zak-20Ar-6i Стеклопакет 1-но камерный энергосберегающий с закалённым стеклом с одной стороны, без солнцезащитного покрытия	///
6-20Ar-6i Стеклопакет 1-но камерный энергосберегающий, без солнцезащитного покрытия	///
6zak-20Ar-6zakRAL7024 Стеклопакет 1-но камерный с закалёнными стёклами, без солнцезащитного покрытия, с обратнокрашенным стеклом RAL-7024 с одной стороны	///
Сенд. 32мм+2мет Сендвич-панель RAL-7024	///

Примечание

- Общие данные смотри лист 2.
- Общие указания смотри лист 3.
- Спецификацию светопрозрачных конструкций смотри лист 25.
- Узлы смотри лист 20-23.
- За отметку 0.000 на фасаде принят уровень чистого пола 1 этажа.
- Каркасы витражей фасадная система TFS 50, дверная серия с терморазрывом TDS 65.
- Вид с фасада здания.
- Фактические размеры конструкций могут отличаться после выполнения геодезической съёмки.
- Покрытие профилей порошковая окраска RAL 7024.

						04-2026/Т-104-КМ			
						"Многоквартирный жилой дом со встроенными помещениями" по адресу: Ленинградская область, Всеволожский район, дер. Новосаратовка, кад. №47:07:0605001:1175 (участок 16 по ППТ)			
Изм.	Кол.	Лист	№ док.	Подпись	Дата	Многоквартирный жилой дом со встроенными помещениями	Стадия	Лист	Листов
Разработал	Степочкин				06.2026		Р	19	
Проверил	Баркалов				06.2026				
Н.контр.	Баркалов				06.2026	ВВ-4.1.ВВ-4.2		ГК "Технология"	

10.06.2026 г.
Инв. № подл.
Подпись и дата
Взам. инв. №
Согласовано:

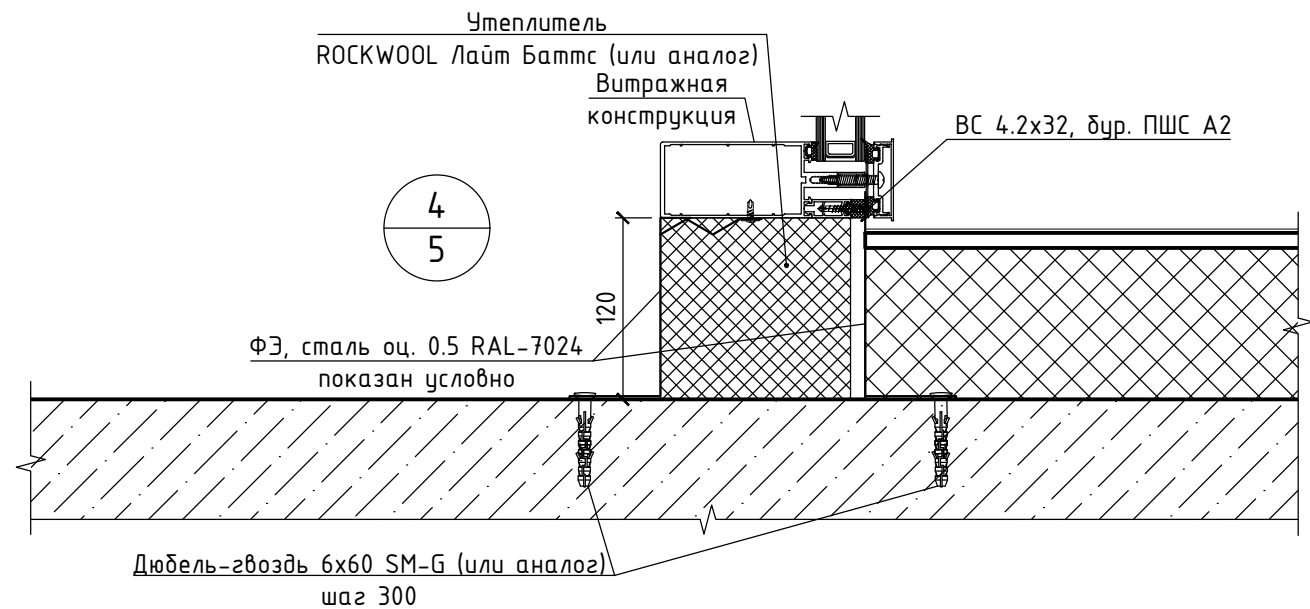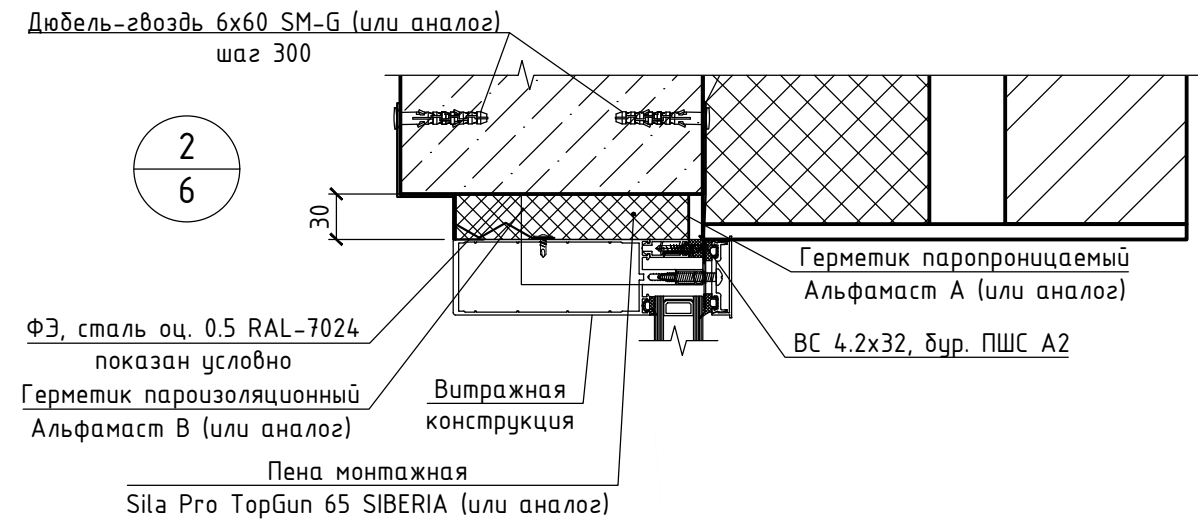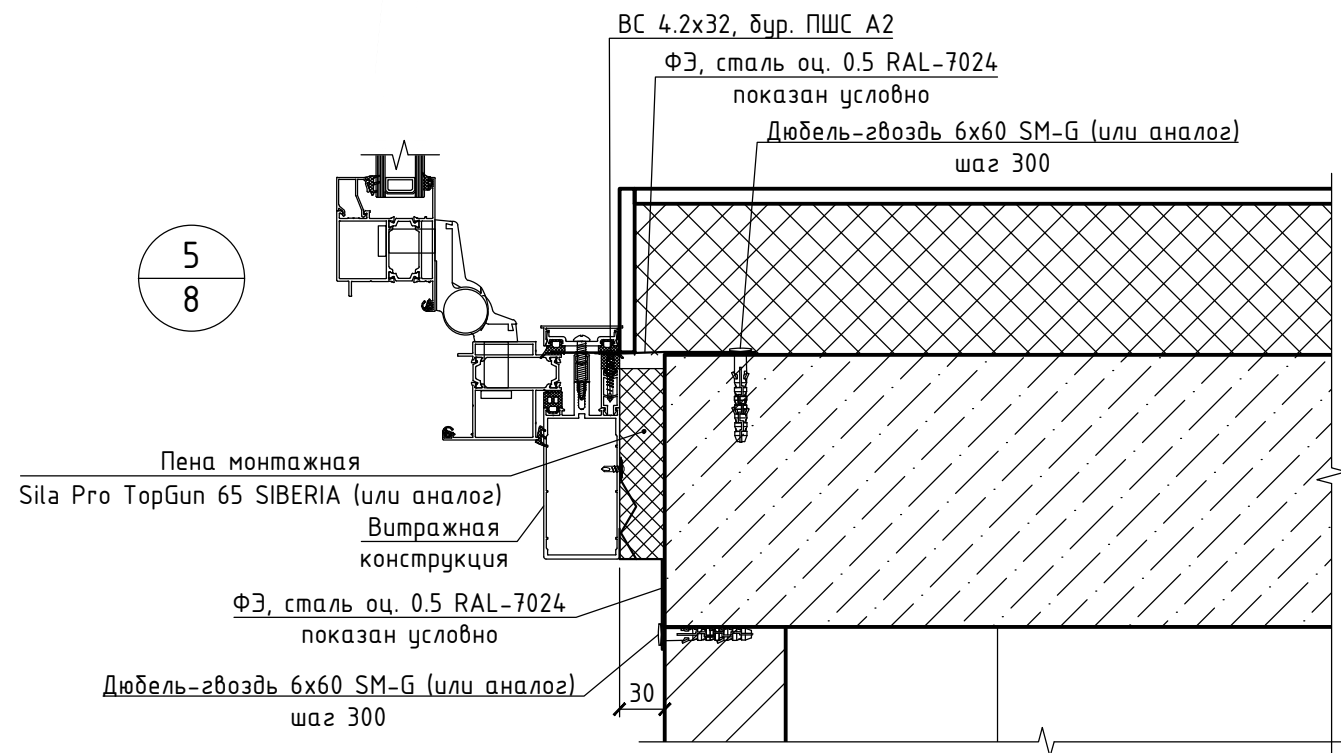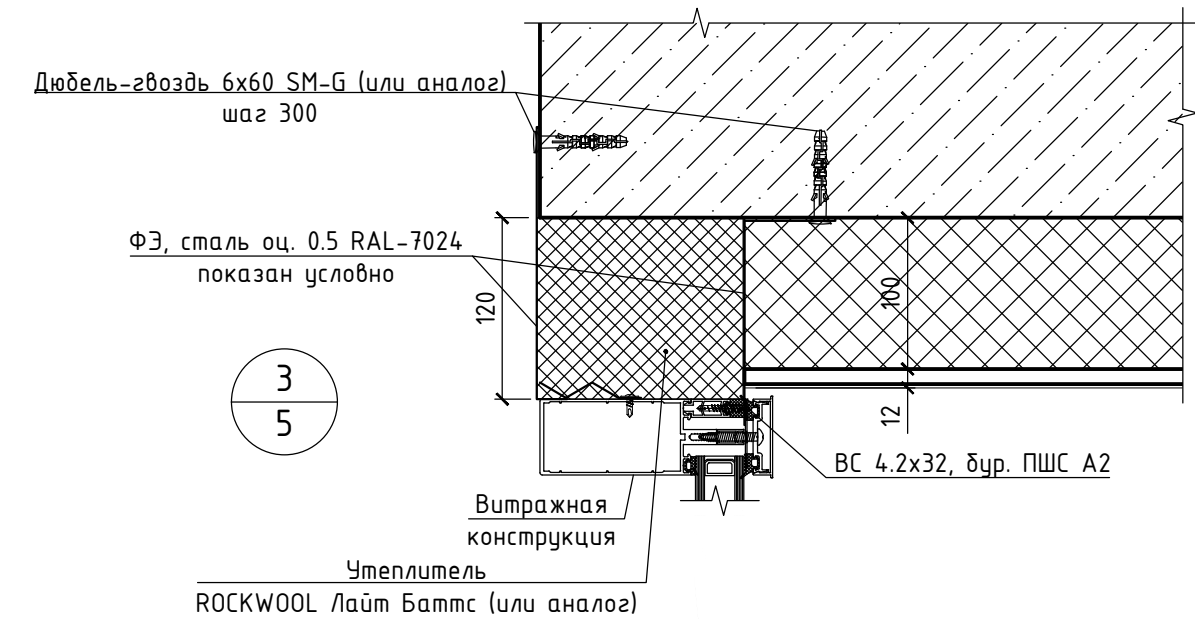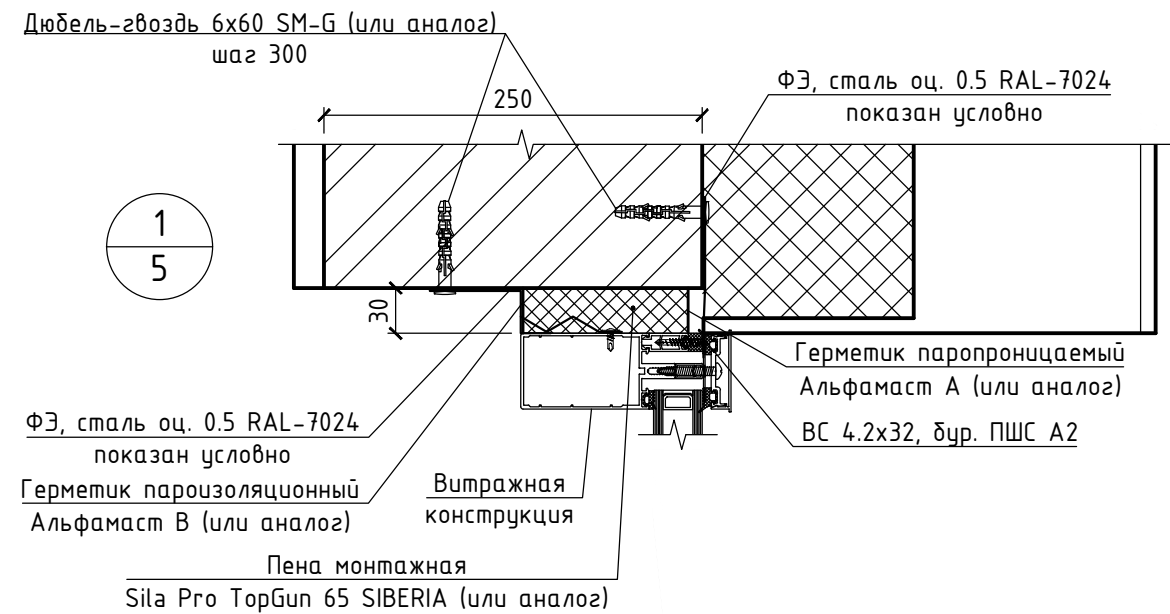

Примечание

- Общие данные смотри лист 2.
- Общие указания смотри лист 3.
- Работать совместно с листами 5-8.





						04-2026/Т-104-КМ			
						"Многоквартирный жилой дом со встроенными помещениями" по адресу: Ленинградская область, Всеволожский район, дер. Новосаратовка, кад. №47:07:0605001:1175 (участок 16 по ППТ)			
Изм.	Кол.	Лист	№ док.	Подпись	Дата	Многоквартирный жилой дом со встроенными помещениями	Стадия	Лист	Листов
Разработал	Степочкин				06.2026		Р	20	
Проверил	Баркалов				06.2026				
Н.контр.	Баркалов				06.2026	Узлы 1-5		ГК "Технология"	

10.06.2026 г.
Инв. № подл.
Подпись и дата
Взам. инв. №

Согласовано:




Примечание

- Общие данные смотри лист 2.
- Общие указания смотри лист 3.
- Работать совместно с листами 9-19.

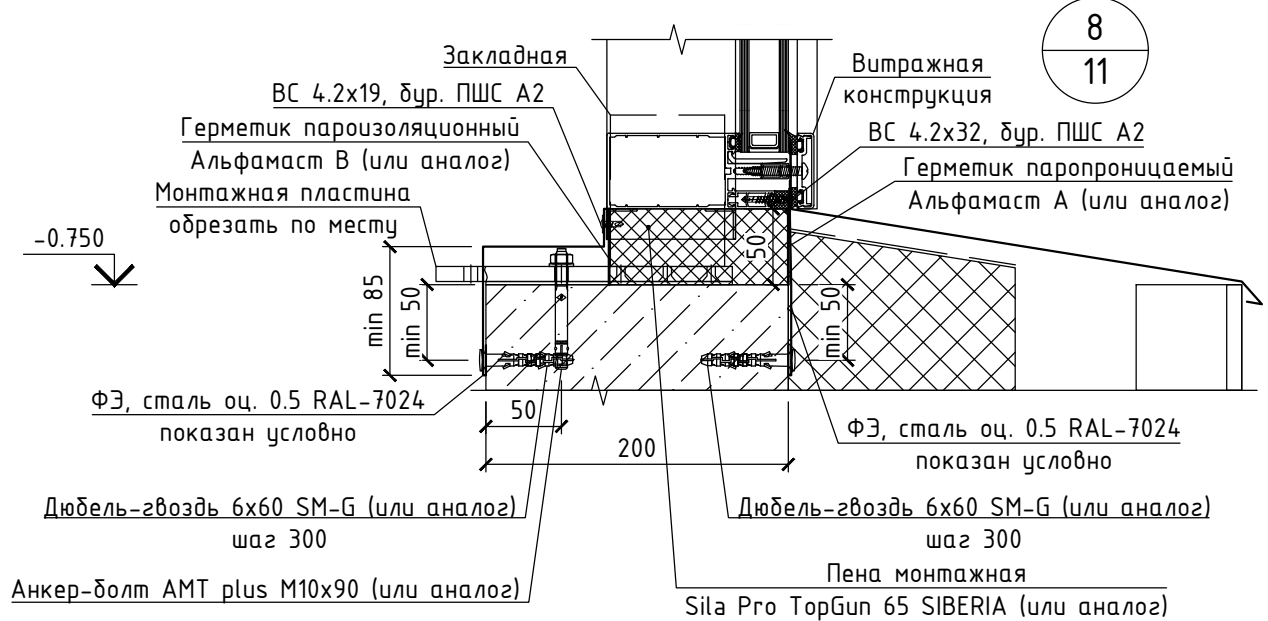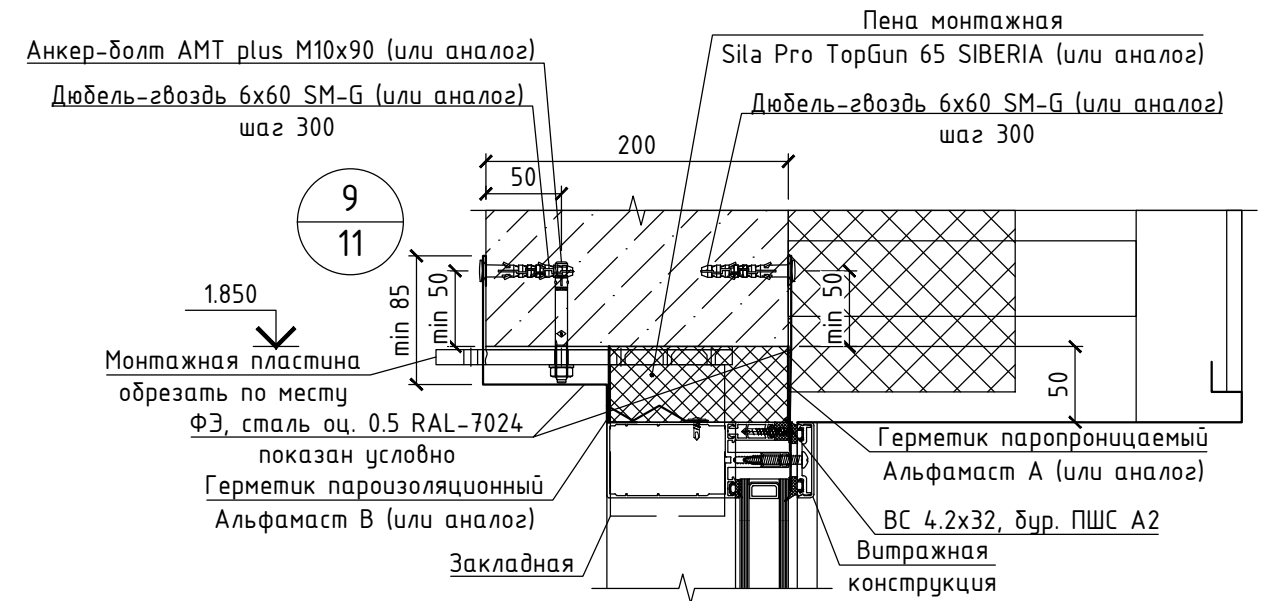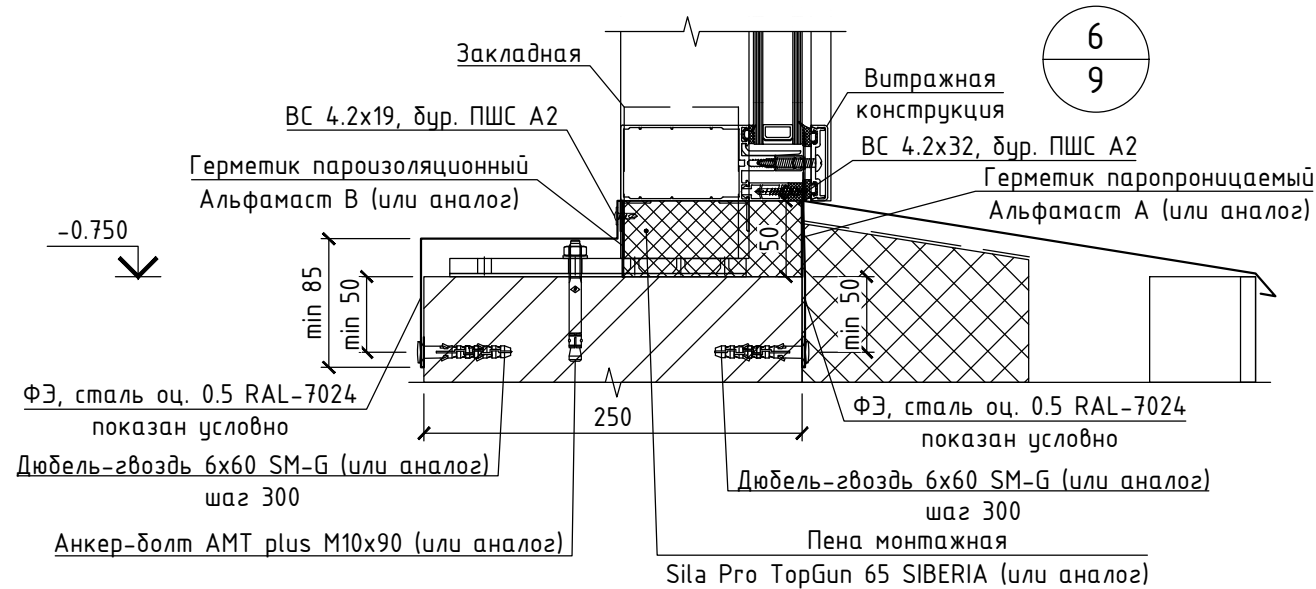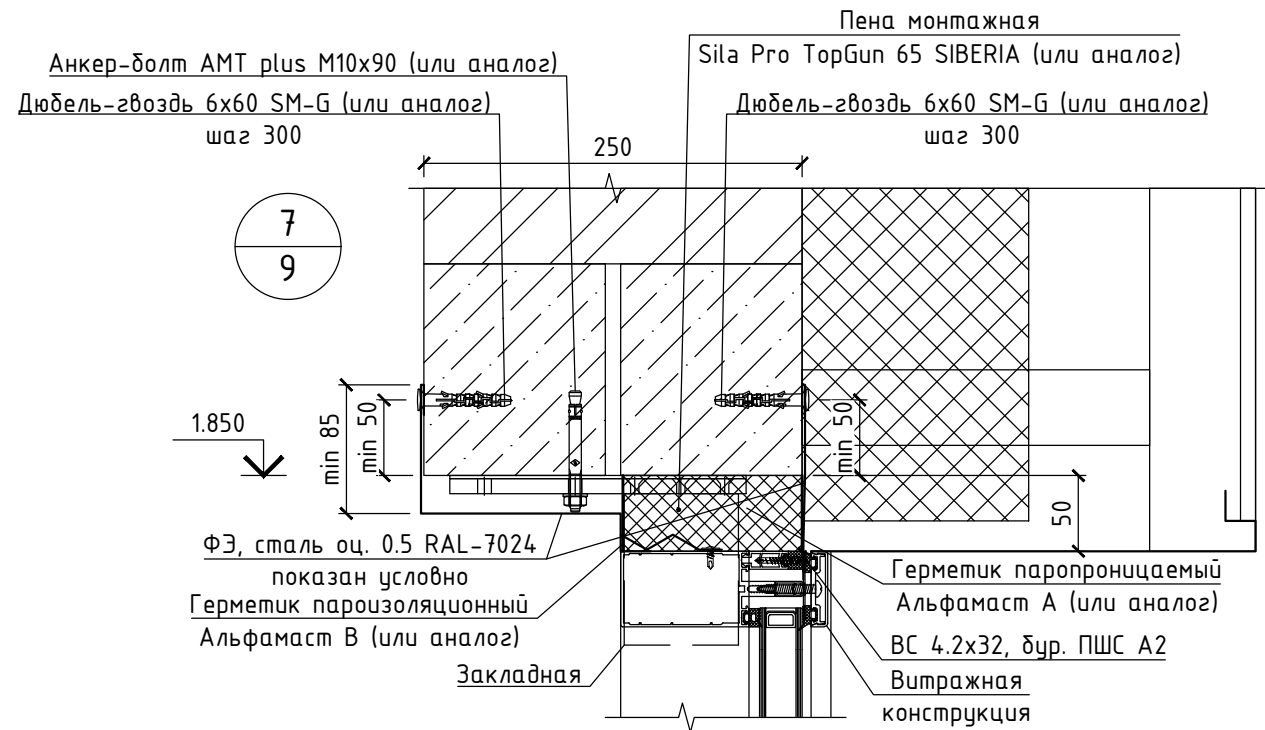

						04-2026/Т-104-КМ			
						"Многоквартирный жилой дом со встроенными помещениями" по адресу: Ленинградская область, Всеволожский район, дер. Новосаратовка, кад. №47:07:0605001:1175 (участок 16 по ППТ)			
Изм.	Кол.	Лист	№ док.	Подпись	Дата	Многоквартирный жилой дом со встроенными помещениями	Стадия	Лист	Листов
Разработал	Степочкин				06.2026		Р	21	
Проверил	Баркалов				06.2026				
Н.контр.	Баркалов				06.2026	Узлы 6-9	ГК "Технология"		

10.06.2026 г.
Инв. № подл.
Подпись и дата
Взам. инв. №

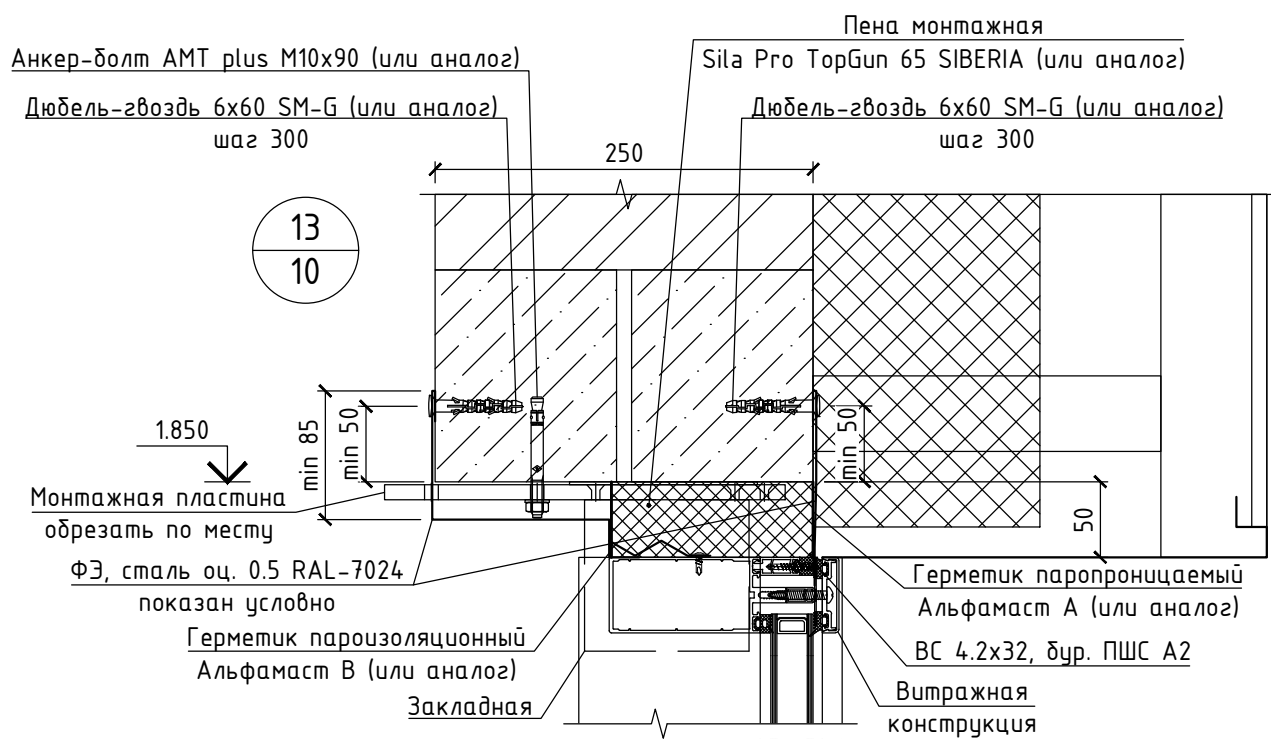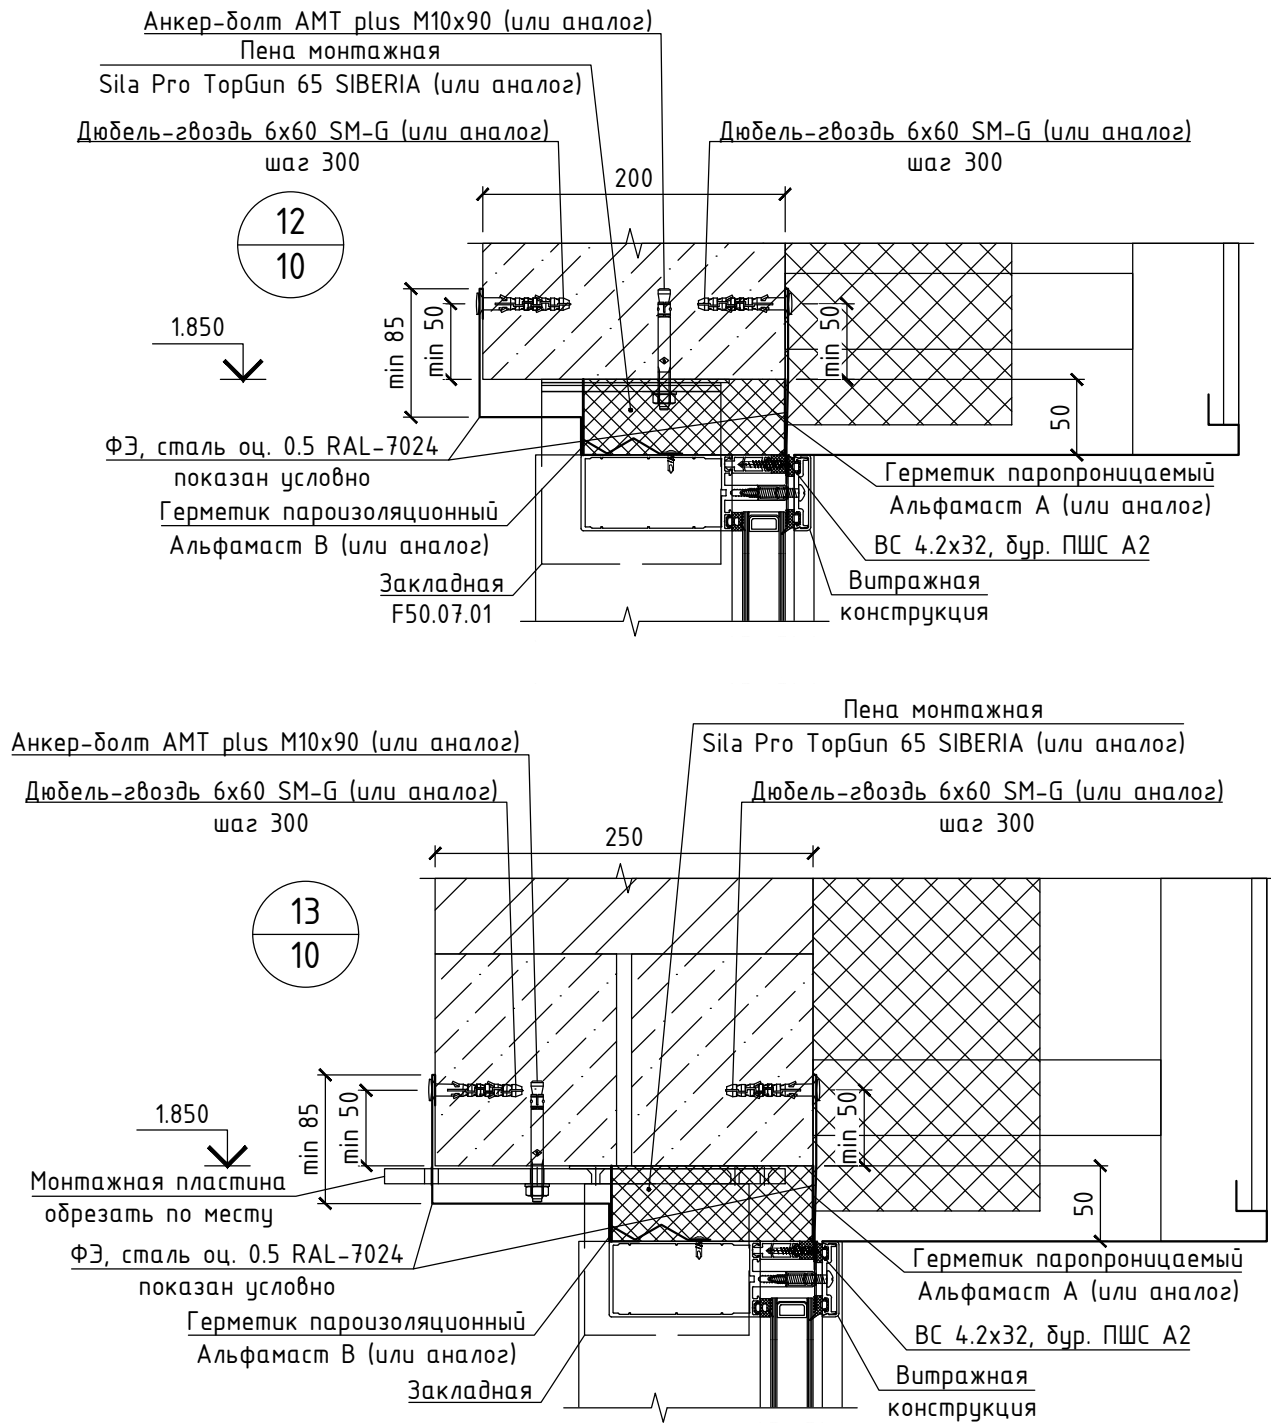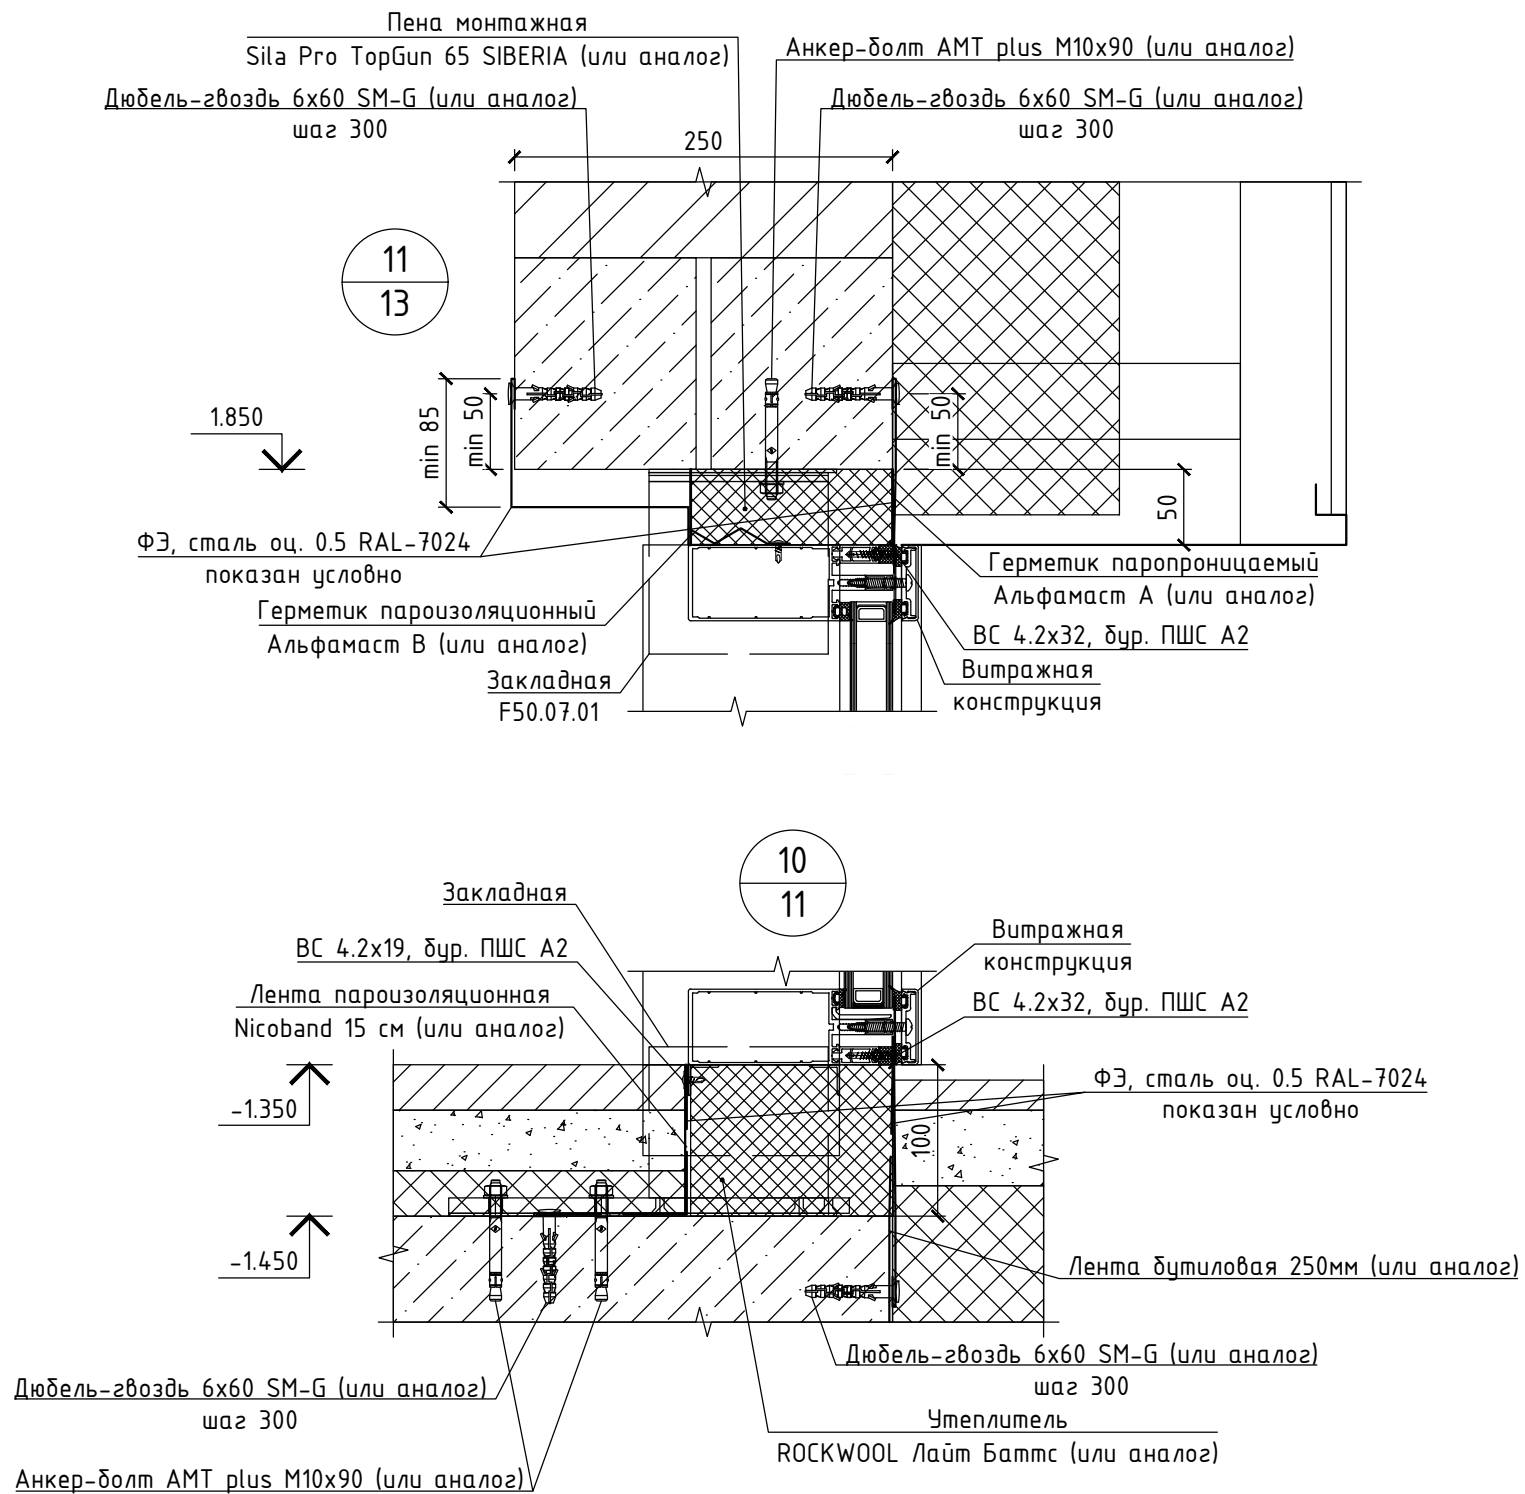

Примечание







1. Общие данные смотри лист 2.
2. Общие указания смотри лист 3.
3. Работать совместно с листами 9-19.
4. Оклеечную гидроизоляцию необходимо нанести без разрыва на всю ширину проёма.

						04-2026/Т-104-КМ			
						"Многоквартирный жилой дом со встроенными помещениями" по адресу: Ленинградская область, Всеволожский район, дер. Новосаратовка, кад. №47:07:0605001:1175 (участок 16 по ППТ)			
Изм.	Кол.	Лист	№ док.	Подпись	Дата	Многоквартирный жилой дом со встроенными помещениями	Стадия	Лист	Листов
Разработал	Степочкин				06.2026		Р	22	
Проверил	Баркалов				06.2026				
Н.контр.	Баркалов				06.2026	Узлы 10-13		ГК "Технология"	

Согласовано:

10.06.2026 г.

Инв. № подл.	Подпись и дата	Взам. инв. №

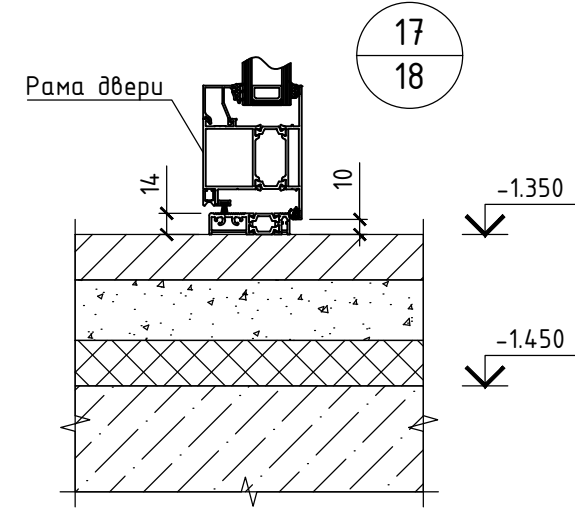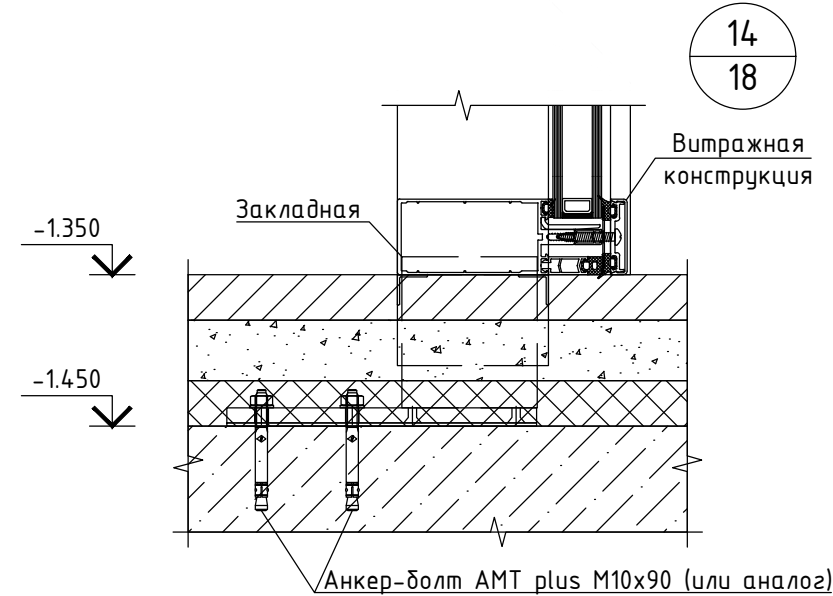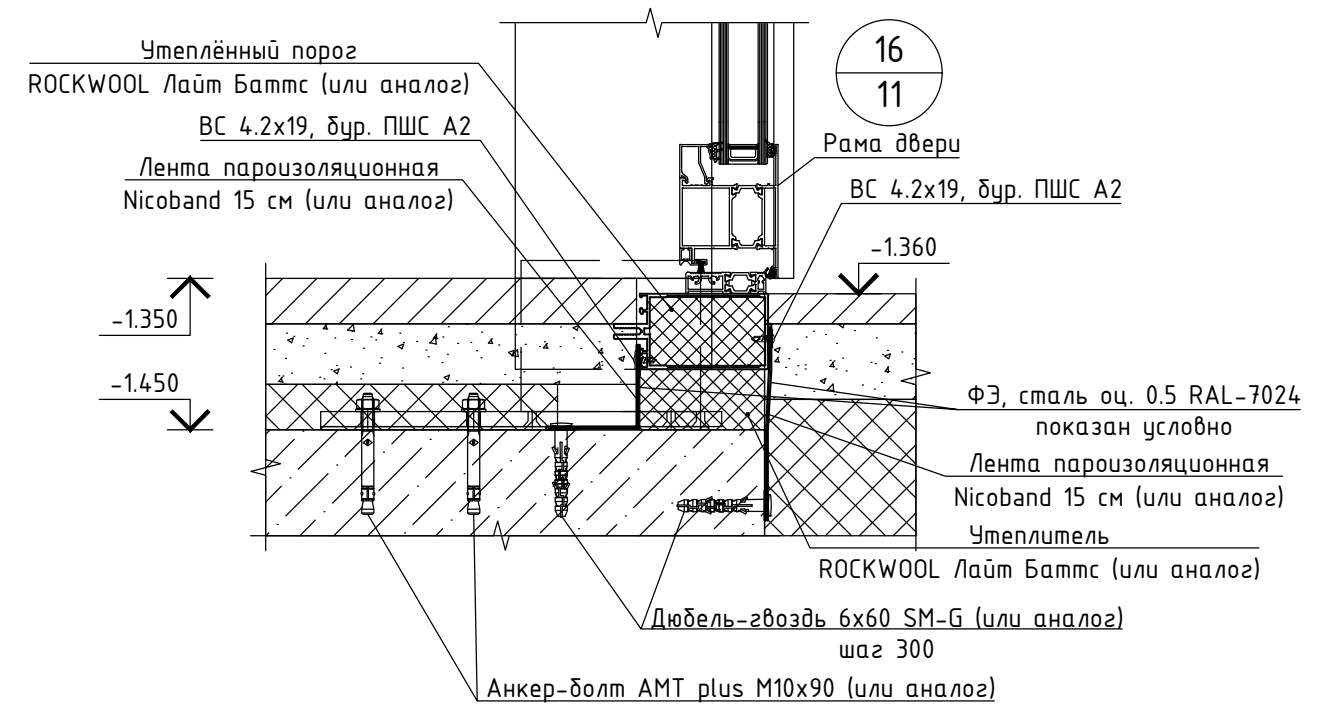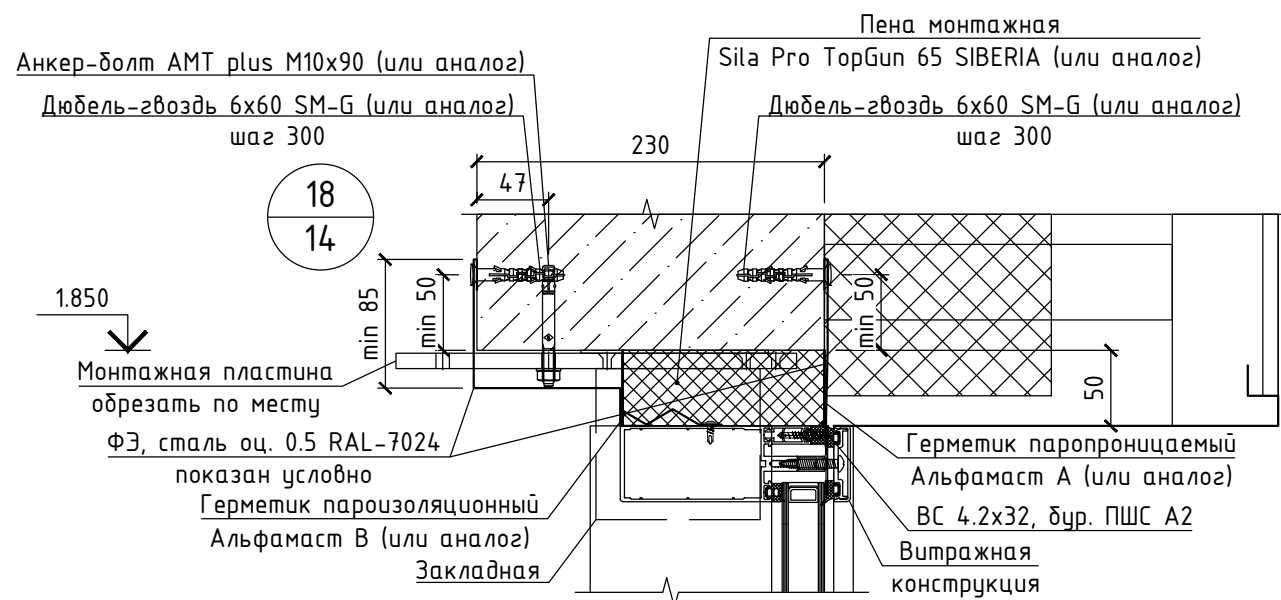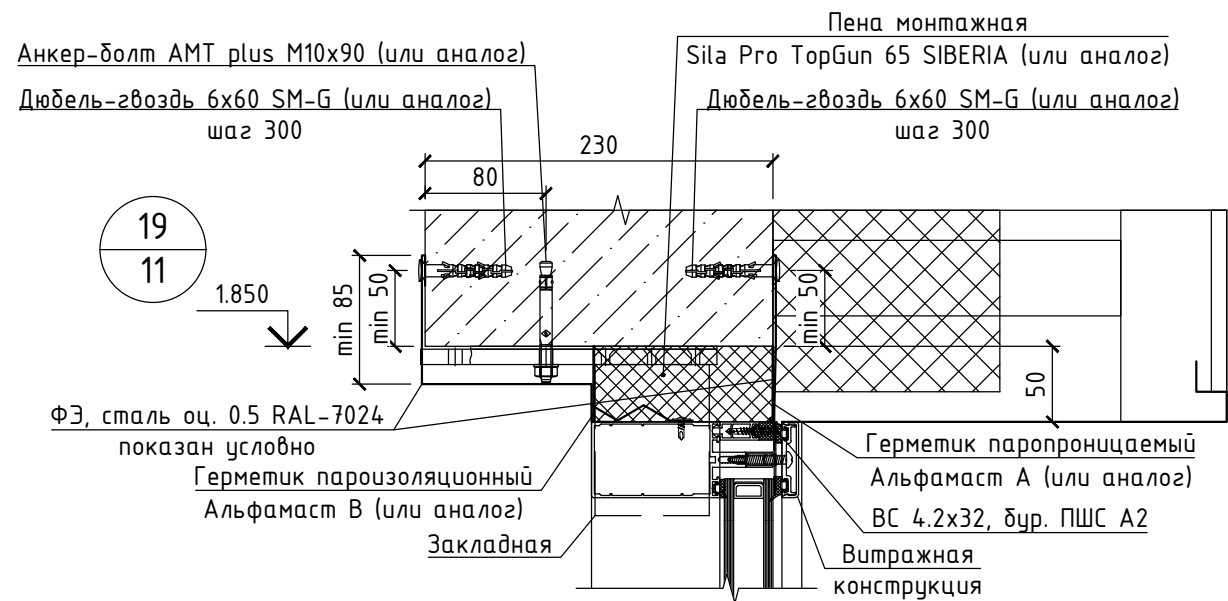
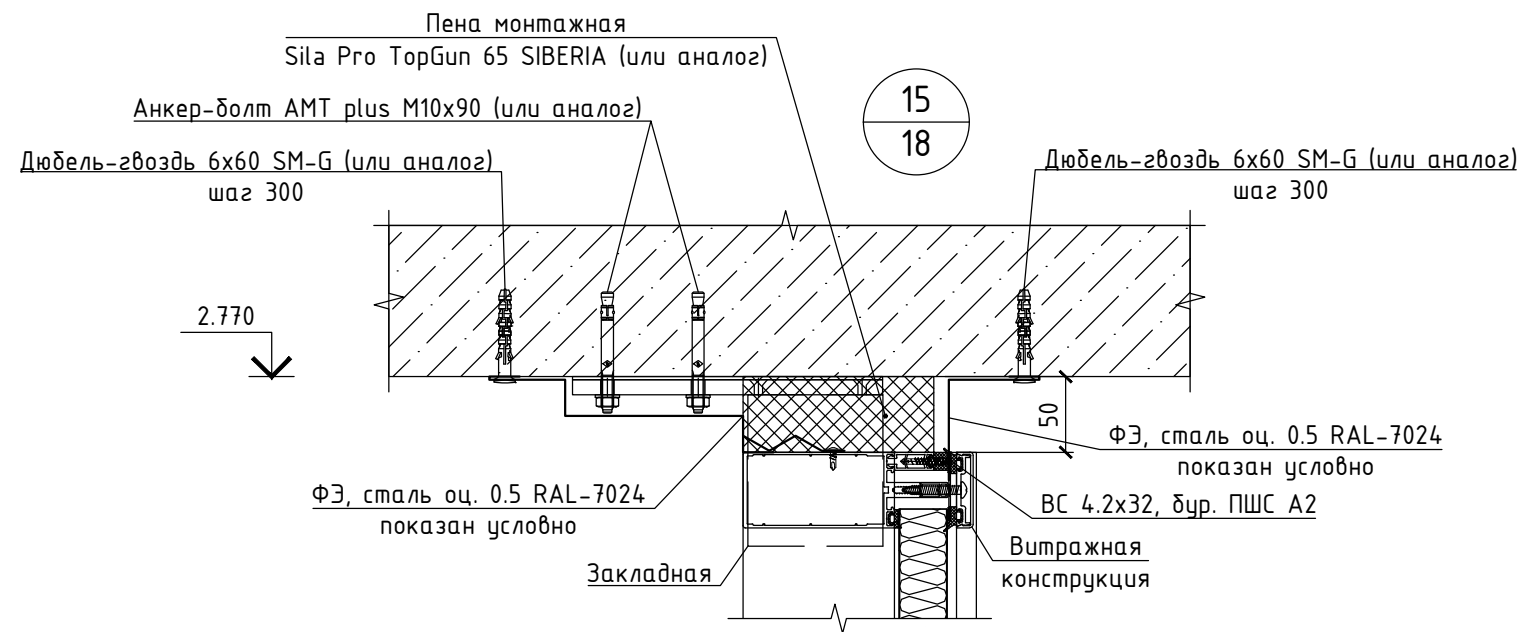


Примечание

- Общие данные смотри лист 2.
- Общие указания смотри лист 3.
- Работать совместно с листами 9-19.
- Оклеенную гидроизоляцию необходимо нанести без разрыва на всю ширину проёма.

						04-2026/Т-104-КМ		
						"Многоквартирный жилой дом со встроенными помещениями" по адресу: Ленинградская область, Всеволожский район, дер. Новосаратовка, кад. №47:07:0605001:1175 (участок 16 по ППТ)		
Изм.	Кол.	Лист	№ док.	Подпись	Дата	Многоквартирный жилой дом со встроенными помещениями	Стадия	Лист
Разработал	Степочкин				06.2026		Р	23
Проверил	Баркалов				06.2026			
Н.контр.	Баркалов				06.2026	Узлы 14-19	ГК "Технология"	

Узел крепления закладной козырька

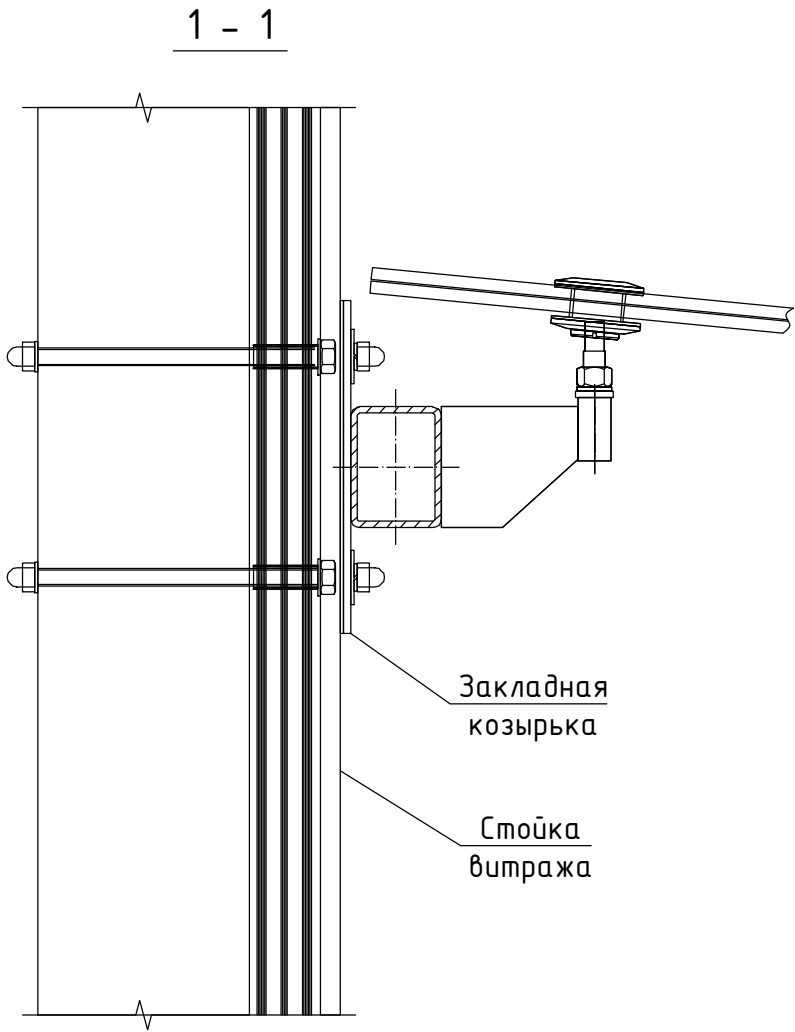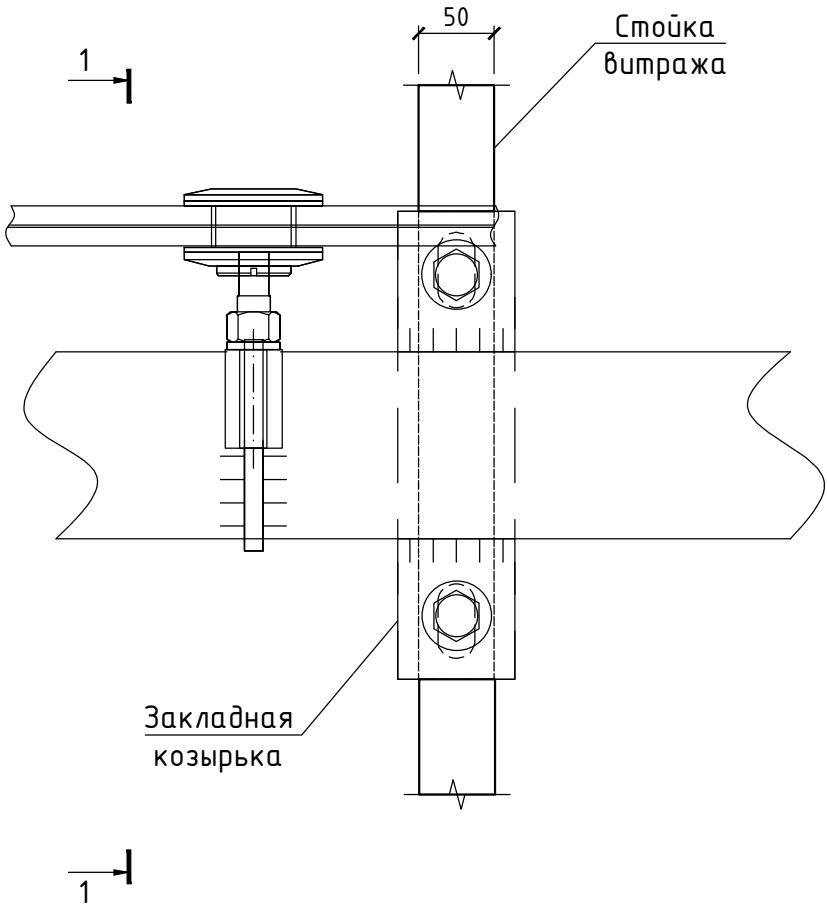

Примечание

1. Общие данные смотри лист 2.
2. Общие указания смотри лист 3.

Согласовано:

10.06.2026 г.

Инв. № подл. Подпись и дата Взам. инв. №

						04-2026/Т-104-КМ			
						"Многоквартирный жилой дом со встроенными помещениями" по адресу: Ленинградская область, Всеволожский район, дер. Новосаратовка, кад. №47:07:0605001:1175 (участок 16 по ППТ)			
Изм.	Кол.	Лист	№ док.	Подпись	Дата	Многоквартирный жилой дом со встроенными помещениями	Стадия	Лист	Листов
Разработал	Степочкин				06.2026		Р	24	
Проверил	Баркалов				06.2026	Узел крепления закладной козырька	ГК "Технология"		
Н.контр.	Баркалов				06.2026				

10.06.2026 г.

Согласовано:

Инд. № подл.

Подпись и дата

Взам. инв. №

Спецификация светопрозрачных конструкций		
Поз.	Описание	Количество
ВН-1.1	Витраж ВН-1.1	1
ВН-1.2	Витраж ВН-1.2	1
ВН-1.3	Витраж ВН-1.3	1
ВН-2.1	Витраж ВН-2.1	1
ВН-2.2	Витраж ВН-2.2	1
ВН-2.3	Витраж ВН-2.3	1
ВН-2.4	Витраж ВН-2.4	9
ВН-2.5	Витраж ВН-2.5	2
ВН-2.6	Витраж ВН-2.6	1
ВН-2.7	Витраж ВН-2.7	1
ВН-3.1	Витраж ВН-3.1	1
ВН-3.2	Витраж ВН-3.2	1
ВН-3.3	Витраж ВН-3.3	1
ВН-3.4	Витраж ВН-3.4	1
ВН-3.5	Витраж ВН-3.5	1
ВН-3.6	Витраж ВН-3.6	2
ВН-3.7	Витраж ВН-3.7	1
ВН-3.8	Витраж ВН-3.8	1
ВН-3.9	Витраж ВН-3.9	1
ВН-4.1	Витраж ВН-4.1	2
ВН-4.2	Витраж ВН-4.2	2
ВН-4.3	Витраж ВН-4.3	1
ВН-4.5	Витраж ВН-4.5	1
ВН-4.6	Витраж ВН-4.6	1
ВН-4.7	Витраж ВН-4.7	1
ВН-4.8	Витраж ВН-4.8	1
ВВ-1.1	Витраж ВВ-1.1	1
ВВ-3.1	Витраж ВВ-3.1	1
ВВ-3.2	Витраж ВВ-3.2	1
ВВ-4.1	Витраж ВВ-4.1	1
ВВ-4.2	Витраж ВВ-4.2	1

Примечание

1. Общие данные смотри лист 2.

2. Общие указания смотри лист 3.

						04-2026/Т-104-КМ			
						"Многоквартирный жилой дом со встроенными помещениями" по адресу: Ленинградская область, Всеволожский район, дер. Новосаратовка, кад. №47:07:0605001:1175 (участок 16 по ППТ)			
Изм.	Кол.	Лист	№ док.	Подпись	Дата				
Разработал	Степочкин				06.2026				
Проверил	Баркалов				06.2026	Многоквартирный жилой дом со встроенными помещениями	Р	25	
Н.контр.	Баркалов				06.2026		Спецификация светопрозрачных конструкций	ГК "Технология"	

Формат А3

Согласовано:				Спецификация алюминиевого профиля	
				Наименование	Цвет	Внутри/снаружи	Ед.изм.	Кол-во	</

Согласовано:

10.06.2026 г.

Взам. инв. №
Подпись и дата
Инв. № подл.

						04-2026/Т-104-КМ				
						"Многоквартирный жилой дом со встроенными помещениями" по адресу: Ленинградская область, Всеволожский район, дер. Новосаратовка, кад. №47:07:0605001:1175 (участок 16 по ППТ)				
Изм.	Кол.	Лист	№ док.	Подпись	Дата					
Разработал		Степочкин			06.2026	Многоквартирный жилой дом со встроенными помещениями		Стадия	Лист	Листов
Проверил		Баркалов			06.2026			Р	26	
Н.контр.		Баркалов			06.2026	Спецификация алюминиевого профиля		ГК "Технология"		

10.06.2026 г.	Инв. № подл.	Подпись и дата	Взам. инв. №

Примечание	
1.	Общие данные смотри лист 2.
2.	Общие указания смотри лист 3.

Формат А3

НО:	Спецификация комплектующих (Продолжение)				
	Наименование		Цвет Внутри/снаружи	Ед.изм.	Кол-во
	D65.13.04 Заглушка стыка створок D65			шт.	42
	D65.13.06 Заглушка сливника D65.07.05 (ЗП)			шт.	54
	F50.09.03 Пластина монтажная 50х196х10 (СРС)			шт.	92
	F50.09.04 Пластина монтажная 50х205х10 (СРС)			шт.	36
	F50.09.05 Пластина монтажная 100х233х10 (СРС)			шт.	14
	F50.09.06 Пластина монтажная 100х265х10 (СРС)			шт.	98
	F50.11.01 Капельник EPDM			шт.	524
	F50.11.08 Дренажная вставка EPDM (СРС)			шт.	546
	F50.12.02 Термовставка 18 мм			м	686
	F50.12.10 Дистанц. Вставка ПВХ 26 мм			м	392
	Нагроон 4.8х70 НТ-R дур (ЗП)			шт.	378
	TAT_BC 4,2X38 DIN 7982 A Винт самонарезающий нерж.			шт.	1121
	TAT_BC 5,5X19 DIN 7981 A Винт самонарезающий нерж. (СРС)			шт.	284
	TAT_BC 5,5X38 DIN 7976 A Винт самонарезающий нерж. (ЗП)			шт.	3418
	TAT_ЛЕНТА БУТ. 40Р Лента бутиловая 40 мм (ЗП)			м	682
	TAT_2.9X19 DIN 7982 A2 Винт самонарезающий нерж.			шт.	216
	TAT_2.9X9.5 DIN 7982 Винт самонарезающий			шт.	81
	TAT_4.2X13 DIN 7981 A2 Винт самонарезающий нерж.			шт.	2400

10.06.2026 г.	Инв. № подл.	Подпись и дата	Взам. инв. №

Спецификация комплектующих (Окончание)			
Наименование	Цвет Внутри/снаружи	Ед.изм.	Кол-во
TAT_4.2X16 DIN 7981 A2 Винт самонарезающий (CPC)		шт.	1092
TAT_4.2X19 DIN 7981 A2 Винт самонарезающий нерж.		шт.	460
TAT_4.2X19 DIN 7982 Винт самонарезающий		шт.	440
TAT_4.2X25 DIN 7982 Винт самонарезающий		шт.	108
TAT_M8 DIN 9081 A2 Шайба (CPC)		шт.	446
TAT_M8X20 DIN 7991 A2 Винт (CPC)		шт.	446
TAT_M8X50 A2 Гайка-штулка соедин. (CPC)		шт.	223
W45.11.02 Уголок уплотнителя W45.10.01		шт.	216
W45.13.04 Крышка дренажного отверстия (ЗП)		шт.	108
W45.16.04 Соединитель угловой литьевой		шт.	162
W65.13.03 Подкладка под зап. TWS/TDS 65 (ЗП)		шт.	216
W65.16.01 Выравнивающий уголок (Артикул только по запросу)		шт.	54

Примечание

1. Общие данные смотри лист 2.
2. Общие указания смотри лист 3.

						04-2026/Т-104-КМ				
						"Многоквартирный жилой дом со встроенными помещениями" по адресу: Ленинградская область, Всеволожский район, дер. Новосаратовка, кад. №47:07:0605001:1175 (участок 16 по ППТ)				
Изм.	Кол.	Лист	№ док.	Подпись	Дата					
Разработал		Степочкин			06.2026	Многоквартирный жилой дом со встроенными помещениями		Стадия	Лист	Листов
Проверил		Баркалов			06.2026			Р	28	
Н.контр.		Баркалов			06.2026	Спецификация комплектующих (Окончание)		ГК "Технология"		

10.06.2026 г.

Инв. № подл.

Подпись и дата

Взам. инв. №

Согласовано:

Спецификация уплотнителя			
Наименование	Цвет Внутри/снаружи	Ед.изм.	Кол-во
F50.10.03 Уплотнитель 3 мм EPDM		м	582,2
F50.10.07 Уплотнитель 7 мм EPDM		м	196,6
F50.10.10 Уплотнитель 10мм EPDM		м	403,9
F50.10.12 Уплотнитель 12мм EPDM		м	166,7
F50.10.18 Уплотнитель прижимной EPDM		м	1374,7
TAT_PB048.0750-FP Уплотнитель щеточный		м	41,2
TAT_PB069.1000-ЗР Уплотнитель щеточный		м	5,9
W45.10.01 Уплотнитель наружный 3 мм		м	271,4
W45.10.02 Уплотнитель притвора		м	474,8
W45.10.03 Уплотнитель внутренний 4.5 мм (ЗП)		м	271,4
W45.10.08 Уплотнитель внутренний 3.5 мм (ЗП)		м	162,6

Примечание

1. Общие данные смотри лист 2.
2. Общие указания смотри лист 3.

						04-2026/Т-104-КМ			
						"Множкквартирный жилой дом со встроенными помещениями" по адресу: Ленинградская область, Всеволожский район, дер. Новосаратовка, кад. №47:07:0605001:1175 (участок 16 по ППТ)			
Изм.	Кол.	Лист	№док.	Подпись	Дата				
Разработал	Степочкин				06.2026	Множкквартирный жилой дом со встроенными помещениями	Стадия	Лист	Листов
Проверил	Баркалов				06.2026		Р	29	
Н.контр.	Баркалов				06.2026	Спецификация уплотнителя	ГК "Технология"		